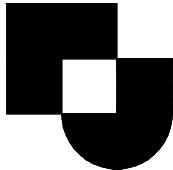


	실장	고문	상무	전무	대표이사
결 재					

DRAWING MANUAL_DETAIL_ver.1

CONSTRUCTION TEAM

2025. 04. 11.



DRAWING LIST

[illegible]

NAME OF CLIENT COMPANY

PROJECT TITLE

DETAIL MANUAL

NOTE

REV.	DATE	DESCRIPTION

NAME OF COMPANY



AJOUDSIGN GROUP

www.ajoudesign.co.kr
서울특별시 강동구 고덕비즈밸리로 6길10
10, Godeok Biz Valley-ro 6-gil, Gangdong-gu,
Seoul, Republic of Korea

DESIGN BY

DRAWING BY

CHECKED BY

DRAWING TITLE

DRAWING LIST

DATE _____

2025. 04.

SCALE

A3:1/ NONE

DRAWING NO.

BD-001

SHEET NO.

DRAWING LIST

SCALE
NONE

1

001

F-001	FINISH DISCRIPTION	CARPET TILE		F-002	FINISH DISCRIPTION	STONE		F-003	FINISH DISCRIPTION	LVT	
F-004	FINISH DISCRIPTION	WOOD FLOORING		F-005	FINISH DISCRIPTION	우레탄 페인트		F-006	FINISH DISCRIPTION	에폭시 페인트	
F-007	FINISH DISCRIPTION	TILE		F-008	FINISH DISCRIPTION	ENTRANCE(DUST MATT)	TILE	F-009	FINISH DISCRIPTION	ROLL CARPET	VINYL TILE

NAME OF CLIENT COMPANY

PROJECT TITLE

DETAIL
MANUAL

NOTE

REV.	DATE	DESCRIPTION

NAME OF COMPANY

www.ajoudesign.co.kr
서울특별시 강동구 고덕비즈밸리로 6길10
10, Godeok Biz Valley-ro 6-gil, Gangdong-gu,
Seoul, Republic of Korea

DESIGN BY
DRAWING BY
CHECKED BY
DRAWING TITLE

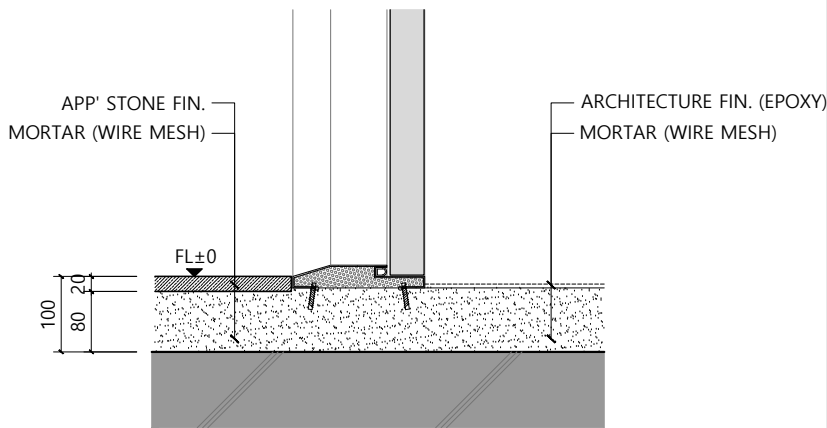
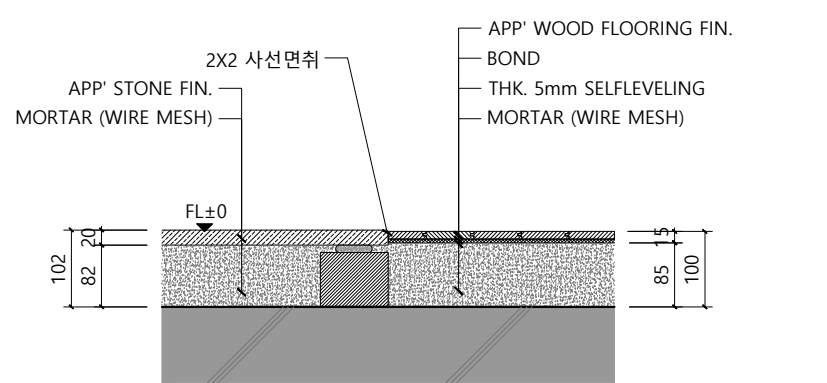
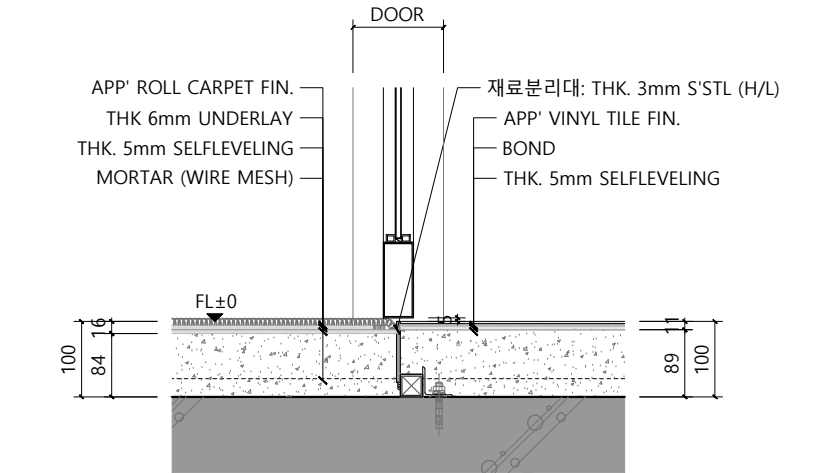
바닥상세도-1

DATE
2025. 04.

SCALE
A3:1/10

DRAWING NO.
FD-001

SHEET NO.
002

												NAME OF CLIENT COMPANY	
												PROJECT TITLE	
												DETAIL MANUAL	
												NOTE	
F-010	FINISH	STONE	ARCHI'	F-011	FINISH	STONE	WOOD FLOORING	F-012	FINISH	ROLL CARPET	VINYL TILE		
	DISCRIPTION				DISCRIPTION				DISCRIPTION				
	FINISH				FINISH				FINISH				
	DISCRIPTION				DISCRIPTION				DISCRIPTION				
	FINISH				FINISH				FINISH				
	DISCRIPTION				DISCRIPTION				DISCRIPTION				
	FINISH				FINISH				FINISH				
	DISCRIPTION				DISCRIPTION				DISCRIPTION				

REV.	DATE	DESCRIPTION

NAME OF COMPANY



AJOUDESIGN GROUP

www.ajoudesign.co.kr
서울특별시 강동구 고덕비즈밸리로 6길10
10, Godeok Biz Valley-ro 6-gil, Gangdong-gu,
Seoul, Republic of Korea

DESIGN BY

-

DRAWING BY

-

CHECKED BY

-

DRAWING TITLE

바닥상세도-2

DATE

2025. 04.

SCALE

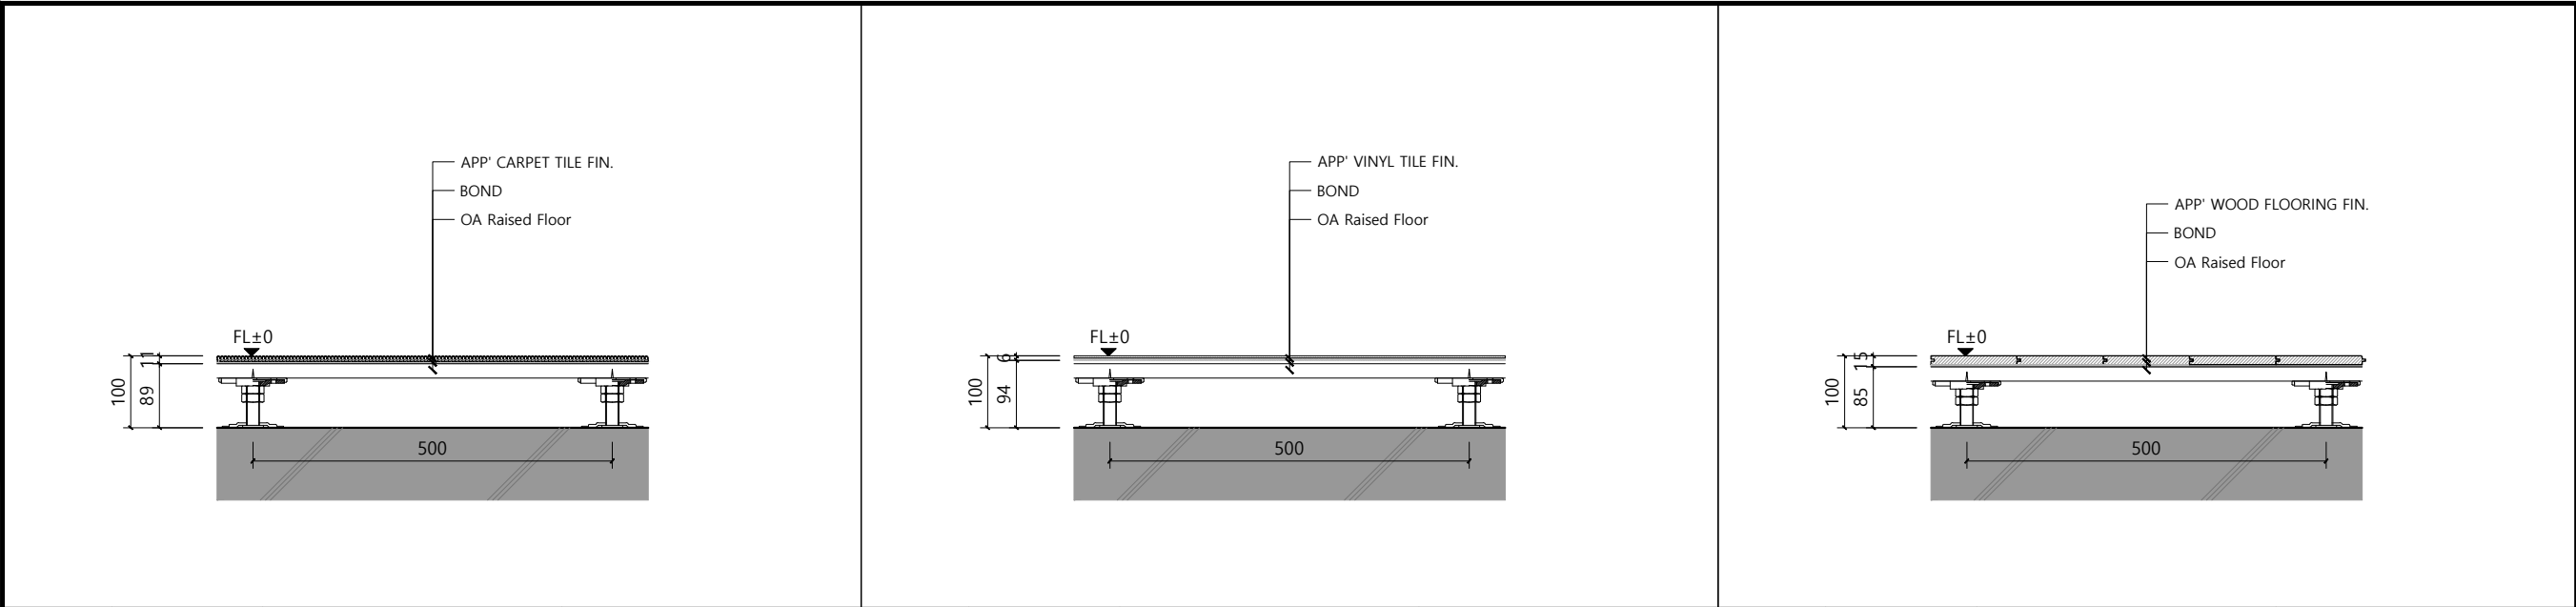
A3:1/10

DRAWING NO.


FD-002

SHEET NO.

003



F-101	FINISH	CARPET TILE	
	DISCRIPTION	OA Raised Floor	
F-102	FINISH	VINYL TILE	
	DISCRIPTION	OA Raised Floor	
F-103	FINISH	WOOD FLOORING	
	DISCRIPTION	OA Raised Floor	

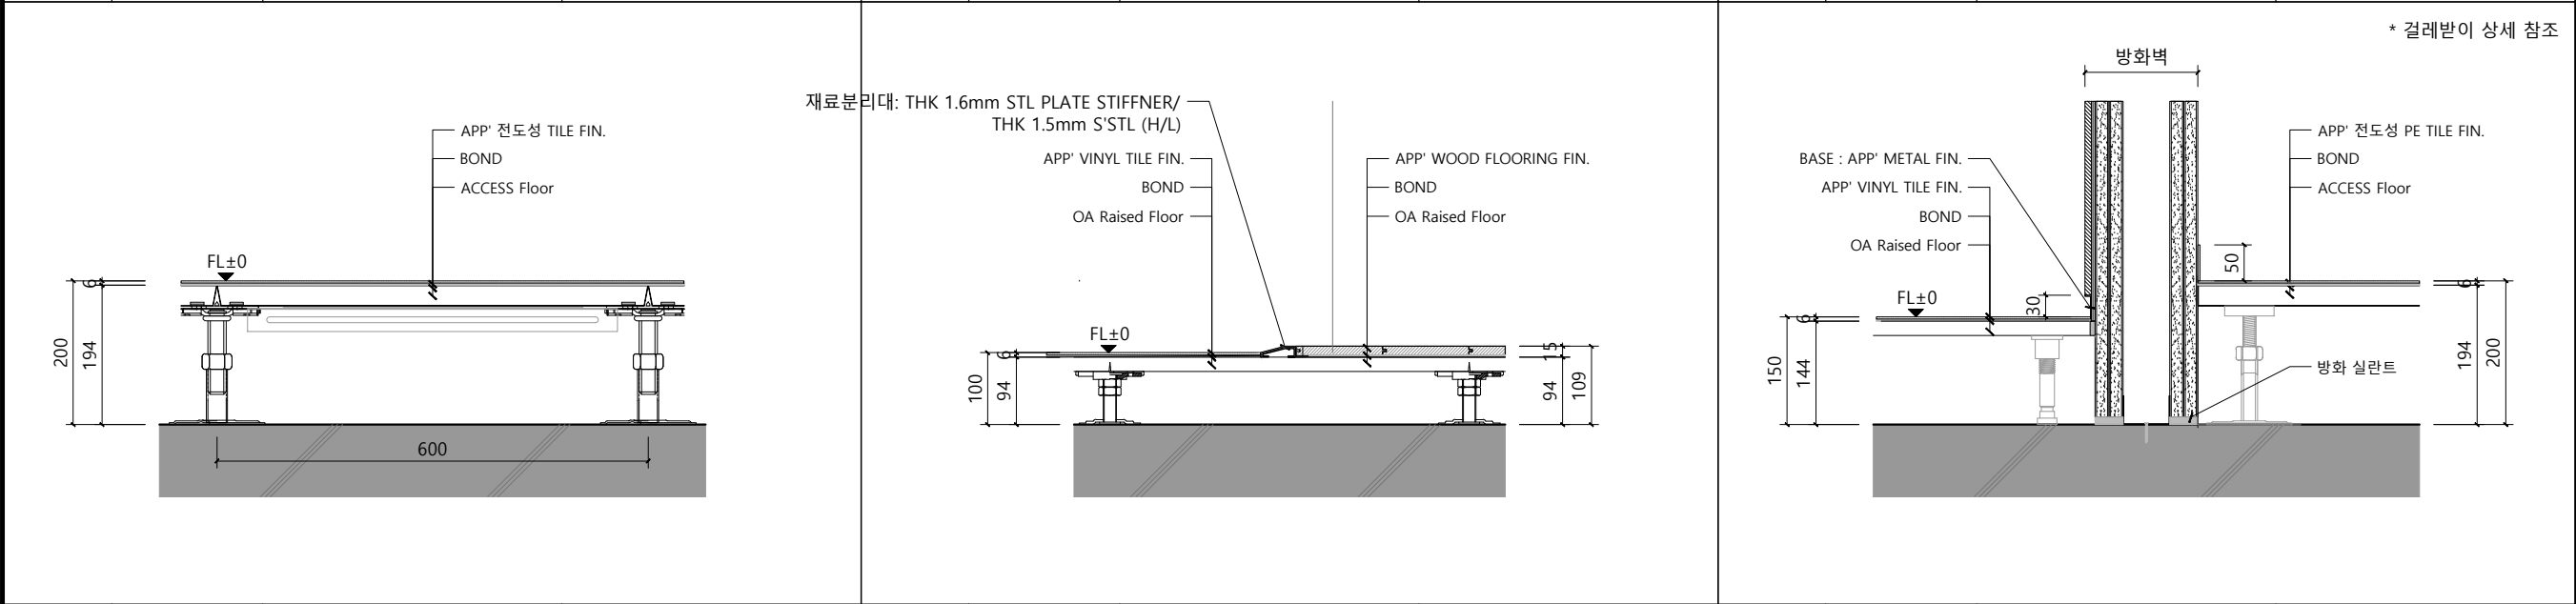

F-104	FINISH	전도성 TILE	
	DISCRIPTION	ACCESS Floor	
F(c)-105	FINISH	VINYL TILE	WOOD FLOORING
	DISCRIPTION	OA Raised Floor	OA Raised Floor
F-106	FINISH	VINYL TILE	전도성 TILE
	DISCRIPTION	OA Raised Floor	ACCESS Floor

	FINISH				FINISH				FINISH		
	DISCRIPTION				DISCRIPTION				DISCRIPTION		

NAME OF CLIENT COMPANY

PROJECT TITLE

DETAIL
MANUAL

NOTE

REV.	DATE	DESCRIPTION

NAME OF COMPANY

www.ajoudesign.co.kr
서울특별시 강동구 고덕비즈밸리로 6길10
10, Godeok Biz Valley-ro 6-gil, Gangdong-gu,
Seoul, Republic of Korea

DESIGN BY

-

DRAWING BY

-

CHECKED BY

-

DRAWING TITLE

바닥상세도-3

DATE

2025. 04.

SCALE

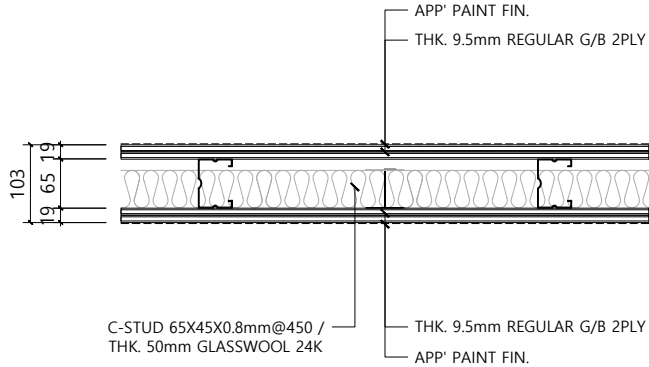
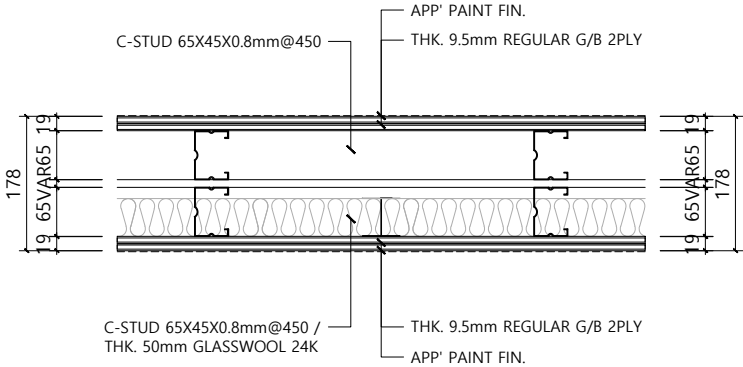
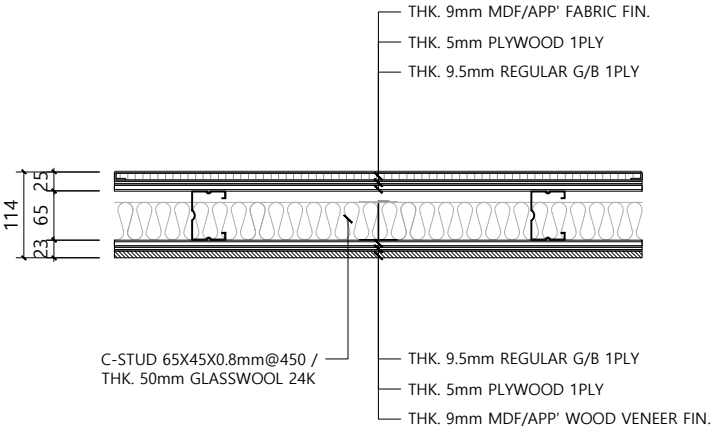
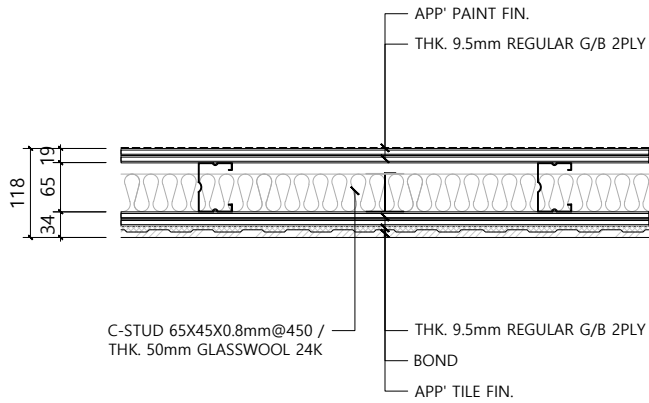
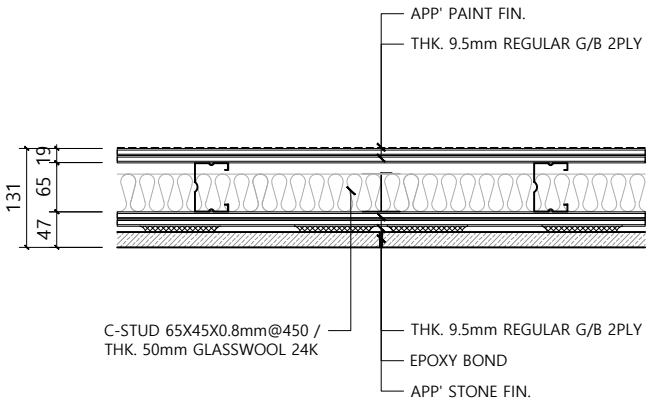
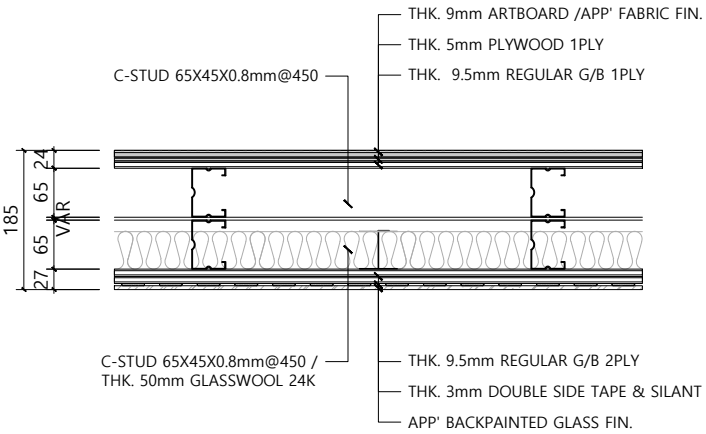
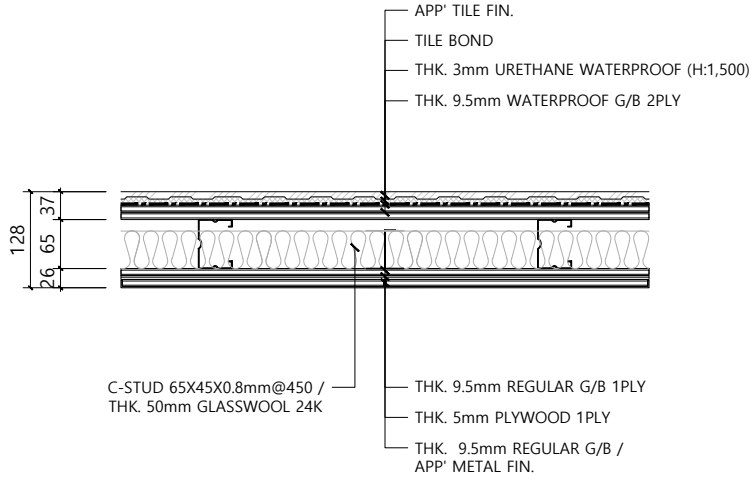
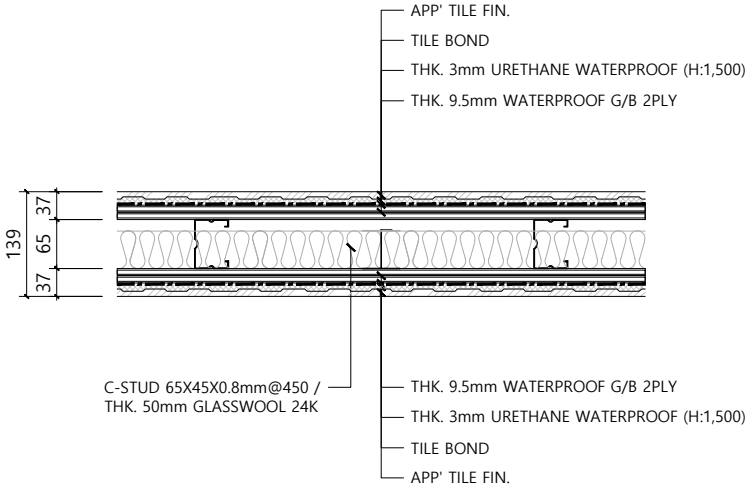
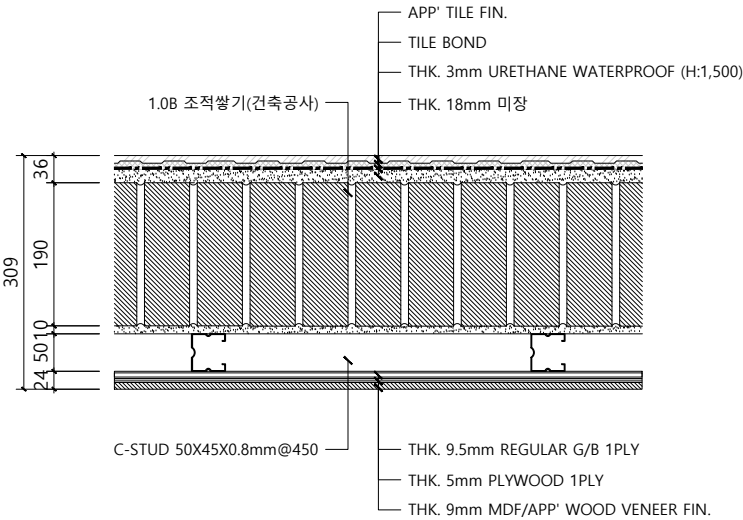
A3:1/10

DRAWING NO.

FD-003

SHEET NO.

004

								
W(C)-001	FINISH	PAINT /PAINT	W(C)-002	FINISH	PAINT /PAINT	W(C)-003	FINISH	WOOD VENEER / FABRIC
	DISCRIPTION	일반 벽체		DISCRIPTION	더블 벽체		DISCRIPTION	일반 벽체
								
W(C)-004	FINISH	PAINT /PAINT	W(C)-005	FINISH	PAINT / STONE	W(C)-006	FINISH	FABRIC(ART BOARD) / GLASS(or MIRROR)
	DISCRIPTION	일반 벽체		DISCRIPTION	일반 벽체		DISCRIPTION	더블 벽체
								
W(C)-007	FINISH	TILE / METAL PANEL	W(C)-008	FINISH	TILE / TILE	W(C)-009	FINISH	TILE / WOOD VENEER
	DISCRIPTION	단면 방수벽체		DISCRIPTION	양면 방수벽체		DISCRIPTION	조적벽

NAME OF CLIENT COMPANY

PROJECT TITLE

DETAIL
MANUAL

NOTE

* 스티드 크기는 경우에 따라 적용

* 인슐레이션은 경우에 따라 적용

* 석고보드 9.5mm 기준(변경가능)

* 합판 5mm 기준(주변마감 고려하여 적용)

*석고 벽체 주의사항

-피스 고정 간격 300mm 이내 조인트 부분 본드 시공

* 벽체 높이 4,000이상일 경우

-□50*50*2.3 STL PIPE 보강

세로보강재-@450/가로보강재-@2,000

REV.	DATE	DESCRIPTION

NAME OF COMPANY



AJOUDESIGN GROUP

www.ajoudesign.co.kr

서울특별시 강동구 고덕비즈밸리로 6길10

10, Godeok Biz Valley-ro 6-gil, Gangdong-gu,

Seoul, Republic of Korea

DESIGN BY

DRAWING BY

CHECKED BY

DRAWING TITLE

벽상세도- 1

DATE

2025. 04.

SCALE

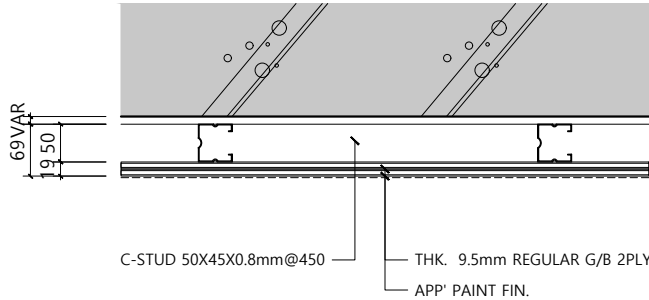
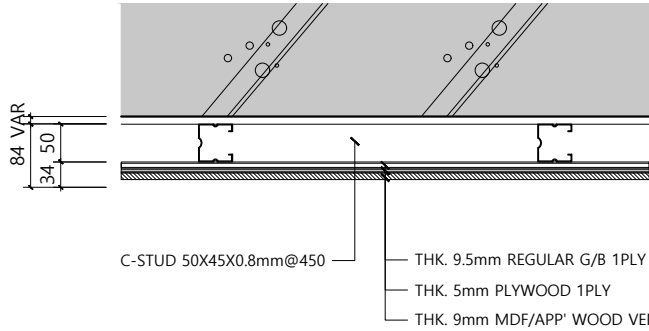
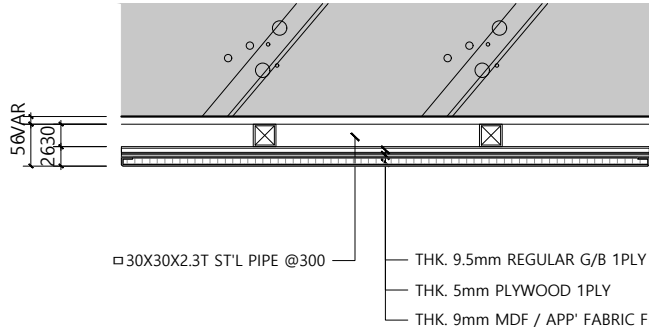
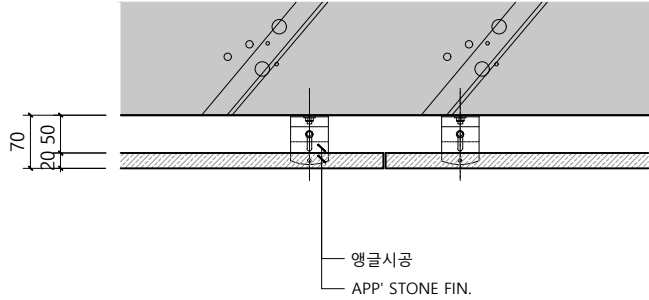
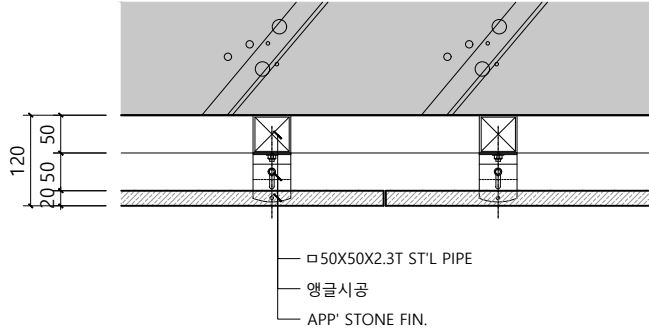
A3:1/10

DRAWING NO.

WD-001

SHEET NO.

006

								
W(C)-101	FINISH	PAINT	W(C)-102	FINISH	WOOD VENEER	W(C)-103	FINISH	FABRIC (각파이프 구조틀)
	DISCRIPTION	단면 벽체		DISCRIPTION	단면 벽체		DISCRIPTION	단면 벽체
								
W-104	FINISH	STONE	W-105	FINISH	STONE		FINISH	
	DISCRIPTION	단면 벽체		DISCRIPTION	단면 벽체		DISCRIPTION	
	FINISH			FINISH			FINISH	
	DISCRIPTION			DISCRIPTION			DISCRIPTION	

NAME OF CLIENT COMPANY

PROJECT TITLE

DETAIL
MANUAL

NOTE

- * 스티드 크기는 경우에 따라 적용
- * 인슐레이션은 경우에 따라 적용
- * 석고보드 9.5mm 기준(변경가능)
- * 합판 5mm 기준(주변 마감 고려하여 적용)

*석고 벽체 주의사항

-피스 고정 간격 300mm 이내 조인트 부분 본드 시공

* 벽체 높이 4,000이상일 경우

-□50*50*2.3 ST'L PIPE 보강

세로보강재-@450/가로보강재-@2,000

REV.	DATE	DESCRIPTION

NAME OF COMPANY



AJOUDESIGN GROUP

www.ajoudesign.co.kr

서울특별시 강동구 고덕비즈밸리로 6길10

10, Godeok Biz Valley-ro 6-gil, Gangdong-gu,

Seoul, Republic of Korea

DESIGN BY

-

DRAWING BY

-

CHECKED BY

-

DRAWING TITLE

벽상세도- 2

DATE

2025. 04.

SCALE

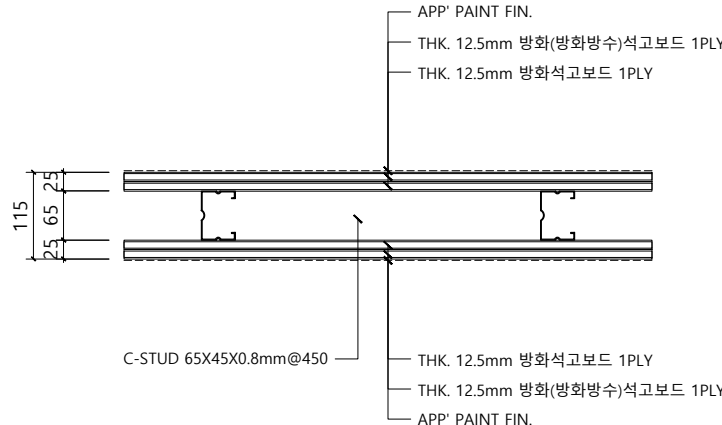
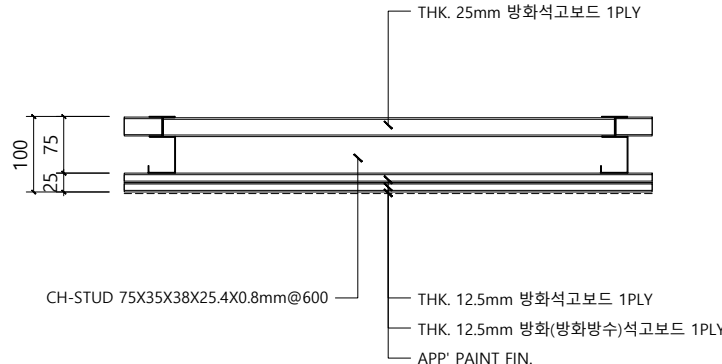
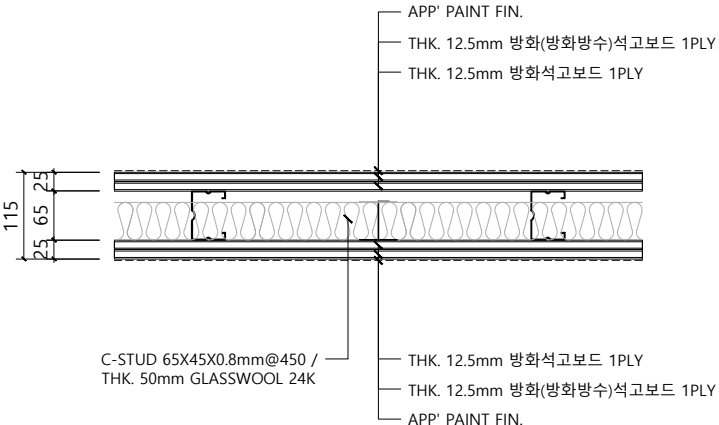
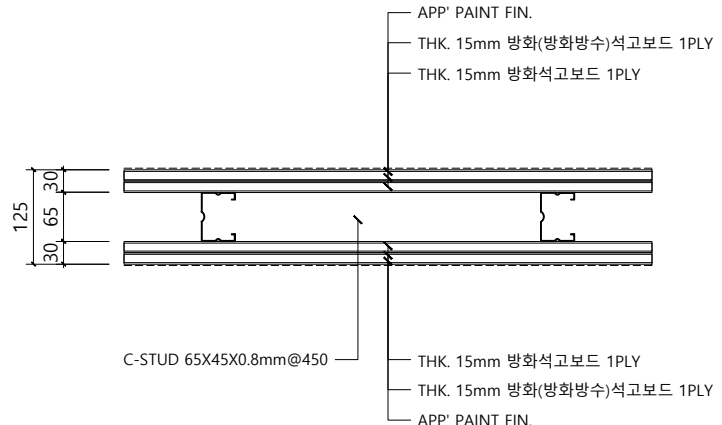
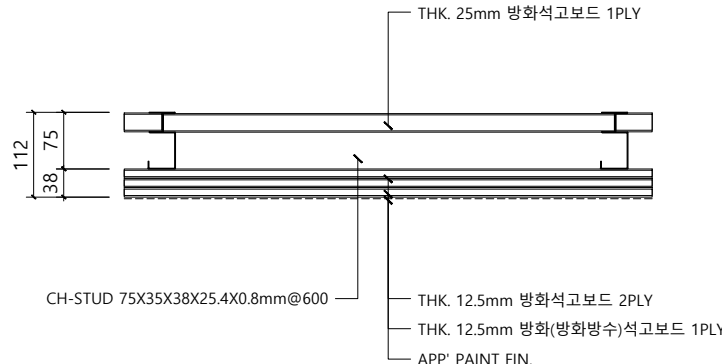
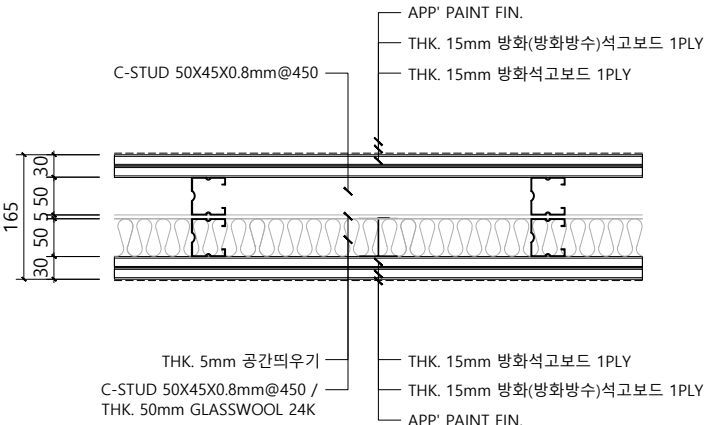
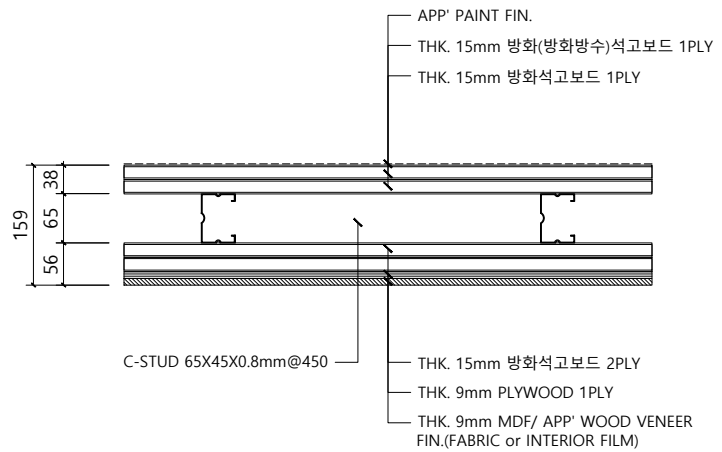
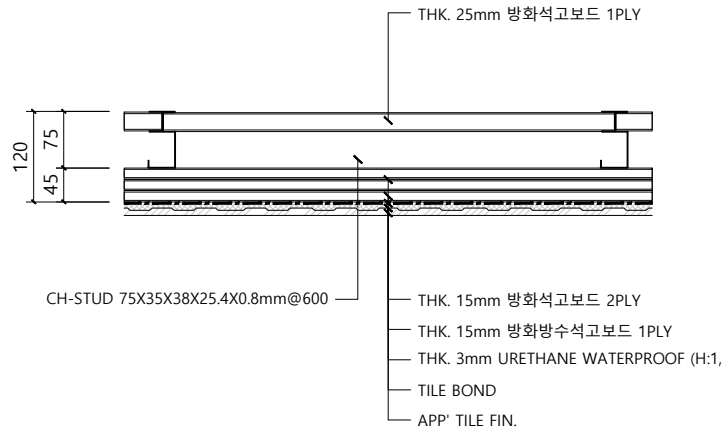
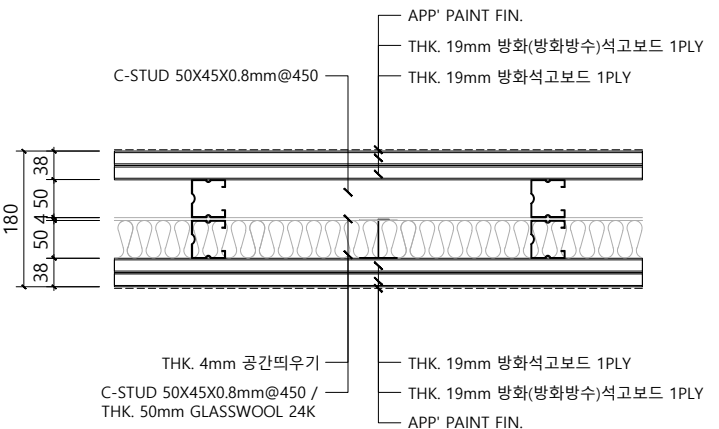
A3:1/10






DRAWING NO.






WD-003

SHEET NO.

007

												NAME OF CLIENT COMPANY	
W-201		FINISH	PAINT / PAINT	W-202		FINISH	PAINT	W-203		FINISH	PAINT /PAINT		
		DISCRIPTION	1시간 내화벽체			DISCRIPTION	1시간 내화벽체			DISCRIPTION	1시간 내화벽체	차음2등급	
												NOTE	
W-204		FINISH	PAINT / PAINT	W-205		FINISH	PAINT / PAINT	W-206		FINISH	PAINT / PAINT		
		DISCRIPTION	1.5시간 내화벽체			DISCRIPTION	1.5시간 내화벽체			DISCRIPTION	1.5시간 내화벽체	차음1등급	
												DETAIL MANUAL	
W-207		FINISH	PAINT / PAINT	W-208		FINISH	PAINT / PAINT	W-209		FINISH	PAINT / PAINT		
		DISCRIPTION	2시간 내화벽체			DISCRIPTION	2시간 내화벽체			DISCRIPTION	2시간 내화벽체	차음1등급	
												PROJECT TITLE	
												DETAIL MANUAL	
												NOTE	
												* KCC 내화성능 기준	
												* 방화구역은 SLAB TO SLAB 시공.	
												* 스타드 크기는 경우에 따라 적용	
												* 인슐레이션은 경우에 따라 적용	
												* 일반 석고보드 9.5mm 기준(변경가능)	
												* 합판 5mm 기준(주변마감 고려하여 적용)	
												* 석고 벽체 주의사항	
												-피스 고정 간격 300mm 이내 조인트 부분 본드 시공	
												* 벽체 높이 4,000이상일 경우	
												-φ50*50*2.3 ST'L PIPE 보강	
												세로보강재-φ450/가로보강재-φ2,000	
												REV.	
												DATE	
												DESCRIPTION	
												NAME OF COMPANY	
													
												AJOUDESIGN GROUP	
												www.ajoudesign.co.kr	
												서울특별시 강동구 고덕비즈밸리로 6길10	
												10, Godeok Biz Valley-ro 6-gil, Gangdong-gu,	
												Seoul, Republic of Korea	
												DESIGN BY	
												DRAWING BY	
												CHECKED BY	
												DRAWING TITLE	
												벽상세도- 3	
												[방화벽]	
												DATE	
												2025. 04.	
												SCALE	
												A3:1/10	
												DRAWING NO.	
												WD-003	
												SHEET NO.	
												008	

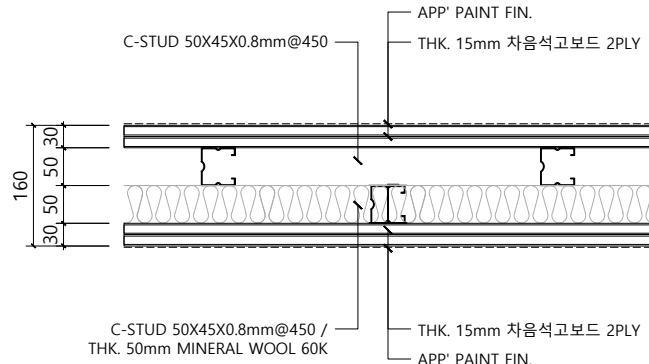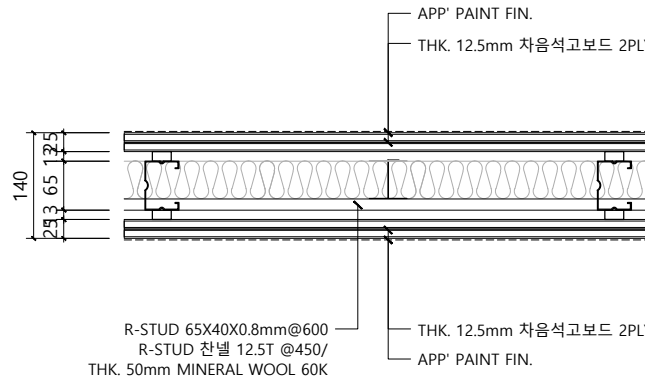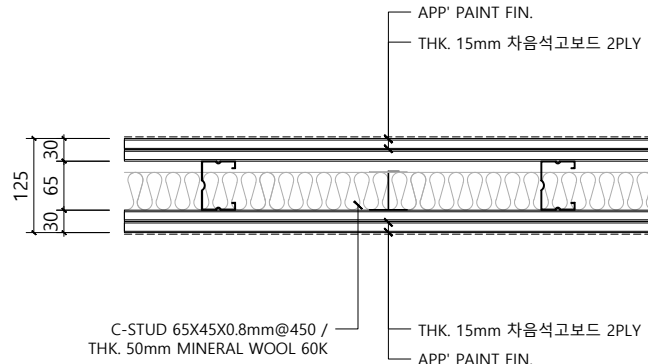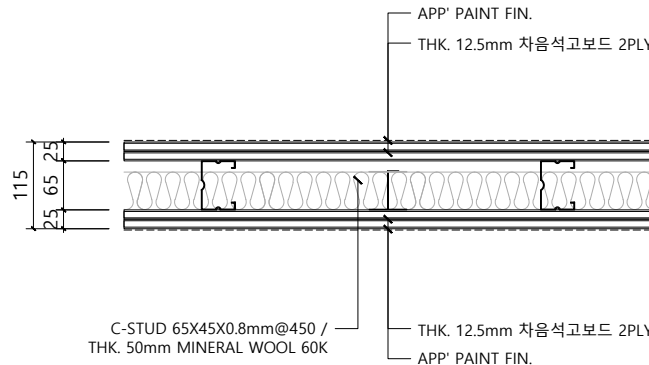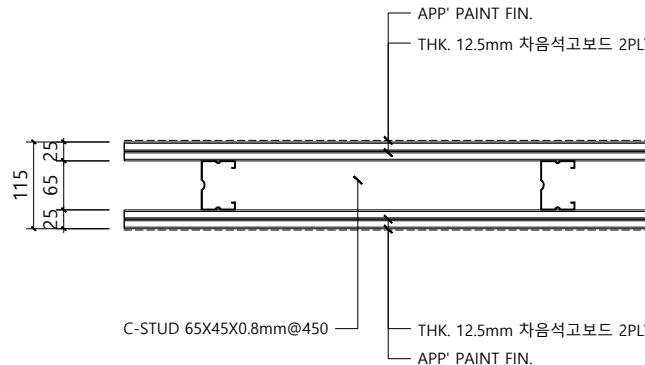												NAME OF CLIENT COMPANY							
												PROJECT TITLE							
												DETAIL MANUAL							
												NOTE							
W-301				W-302				W-303				* KCC 차음성능 기준							
FINISH		PAINT / PAINT		FINISH		PAINT / PAINT		FINISH		PAINT / PAINT		* 스티드 크기는 경우에 따라 적용							
DISCRIPTION		STC64/RW64		DISCRIPTION		STC60/RW62		DISCRIPTION		STC48/RW52		* 안슐레이션은 경우에 따라 적용							
		차음벽체				차음벽체				차음벽체		* 석고보드 9.5mm 기준(변경가능)							
												* 락판 5mm 기준(주변마감 고려하여 적용)							
												* 석고 벽체 주의사항							
												-피스 고정 간격 300mm 이내 조인트 부분 본드 시공							
												* 벽체 높이 4,000이상일 경우							
												-□50*50*2.3 ST.L PIPE 보강							
												세로보강재-@450/가로보강재-@2,000							
FINISH		PAINT / PAINT		FINISH		PAINT / PAINT		FINISH		PAINT / PAINT		REV.							
DISCRIPTION		STC49/RW50		DISCRIPTION		STC46/RW46		DISCRIPTION				DATE							
		차음벽체				차음벽체						DESCRIPTION							
												NAME OF COMPANY							
																			
												AJOUDESIGN GROUP							
												www.ajoudesign.co.kr							
												서울특별시 강동구 고덕비즈밸리로 6길10							
												10, Godeok Biz Valley-ro 6-gil, Gangdong-gu,							
												Seoul, Republic of Korea							
												DESIGN BY							
												DRAWING BY							
												CHECKED BY							
												DRAWING TITLE							
												벽상세도- 4							
												[차음벽]							
												DATE							
												2025. 04.							
												SCALE							
												A3:1/10							
												DRAWING NO.							
												WD-004							
FINISH								FINISH						FINISH				SHEET NO.	
DISCRIPTION								DISCRIPTION						DISCRIPTION				009	

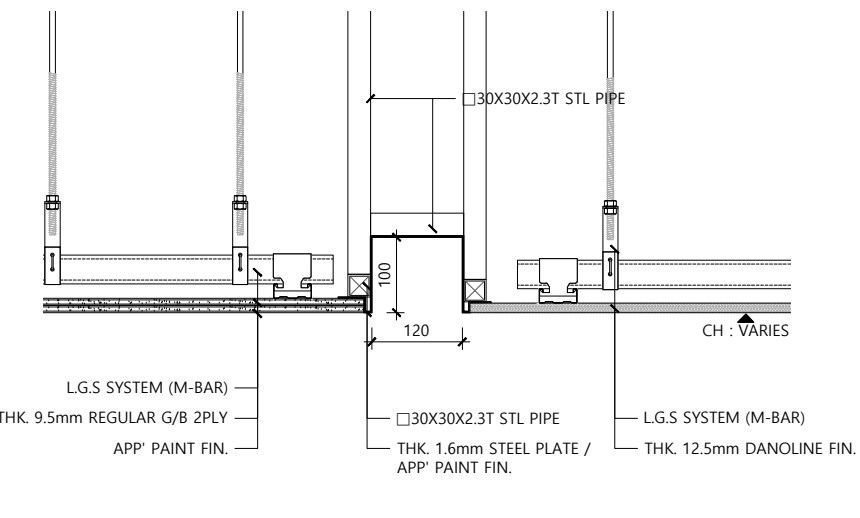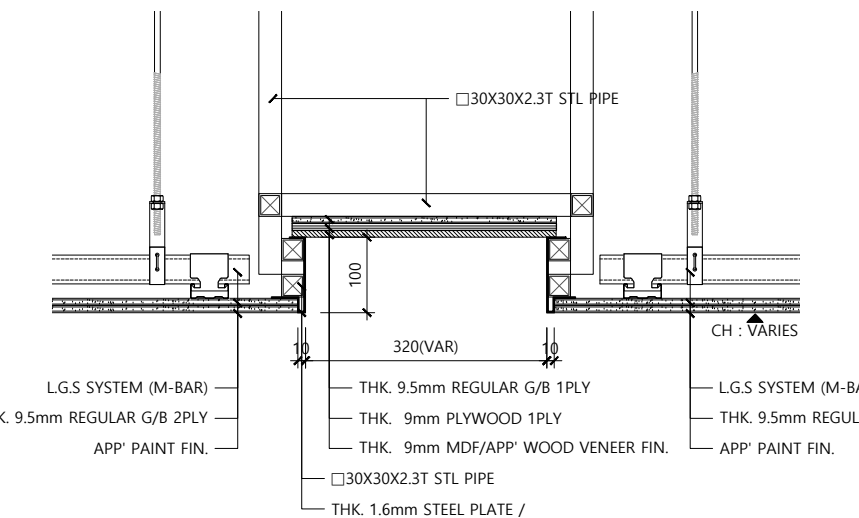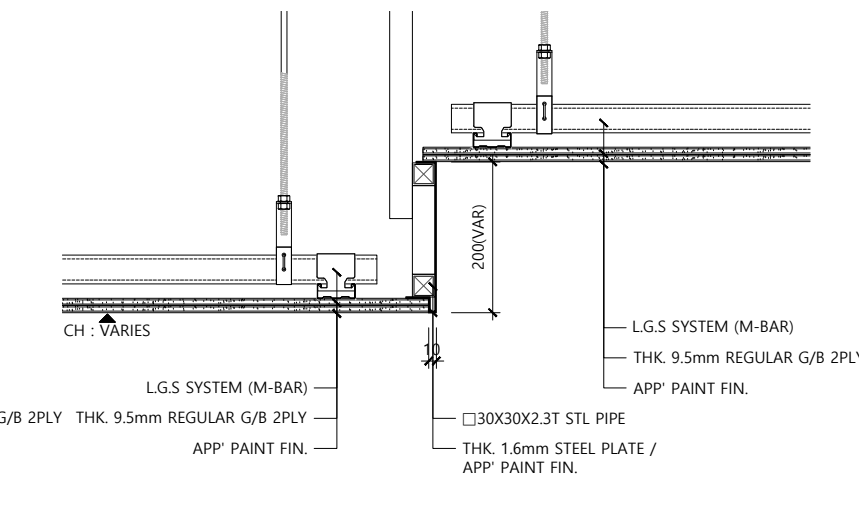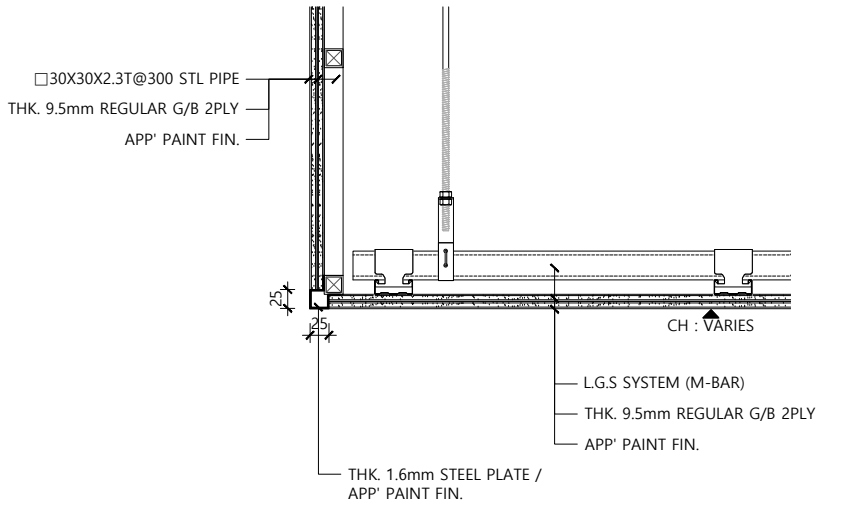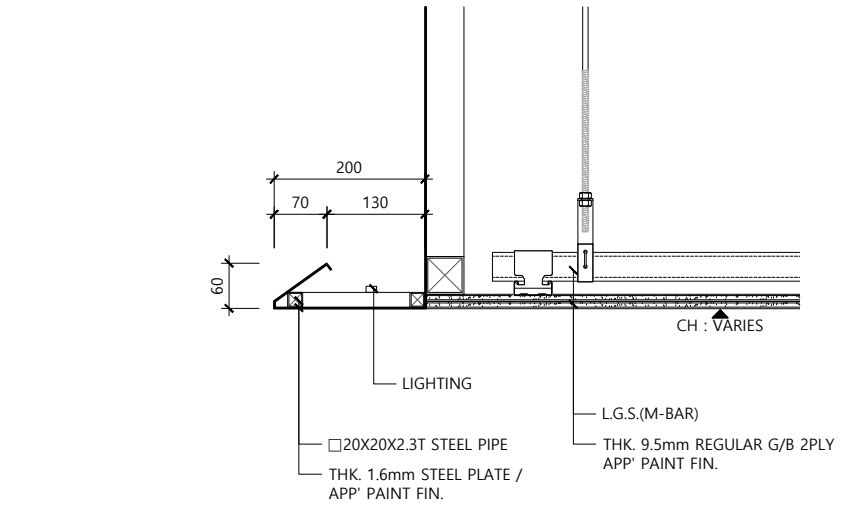								
C-301	FINISH	단천정	C-302	FINISH	단천정	C-303	FINISH	단천정
	DISCRIPTION			DISCRIPTION			DISCRIPTION	
								
C-304	FINISH	단천정	C-305	FINISH	단천정		FINISH	
	DISCRIPTION	노출천정 연결구간		DISCRIPTION	노출천정 연결구간		DISCRIPTION	
	FINISH			FINISH			FINISH	
	DISCRIPTION			DISCRIPTION			DISCRIPTION	

NAME OF CLIENT COMPANY

PROJECT TITLE

DETAIL
MANUAL

NOTE

REV.	DATE	DESCRIPTION

NAME OF COMPANY



AJOUDESIGN GROUP
www.ajoudesign.co.kr
서울특별시 강동구 고덕비즈밸리로 6길10
10, Godeok Biz Valley-ro 6-gil, Gangdong-gu,
Seoul, Republic of Korea

DESIGN BY

-

DRAWING BY

-

CHECKED BY

-

DRAWING TITLE

천정상세도 - 4

DATE

2025. 04.

SCALE

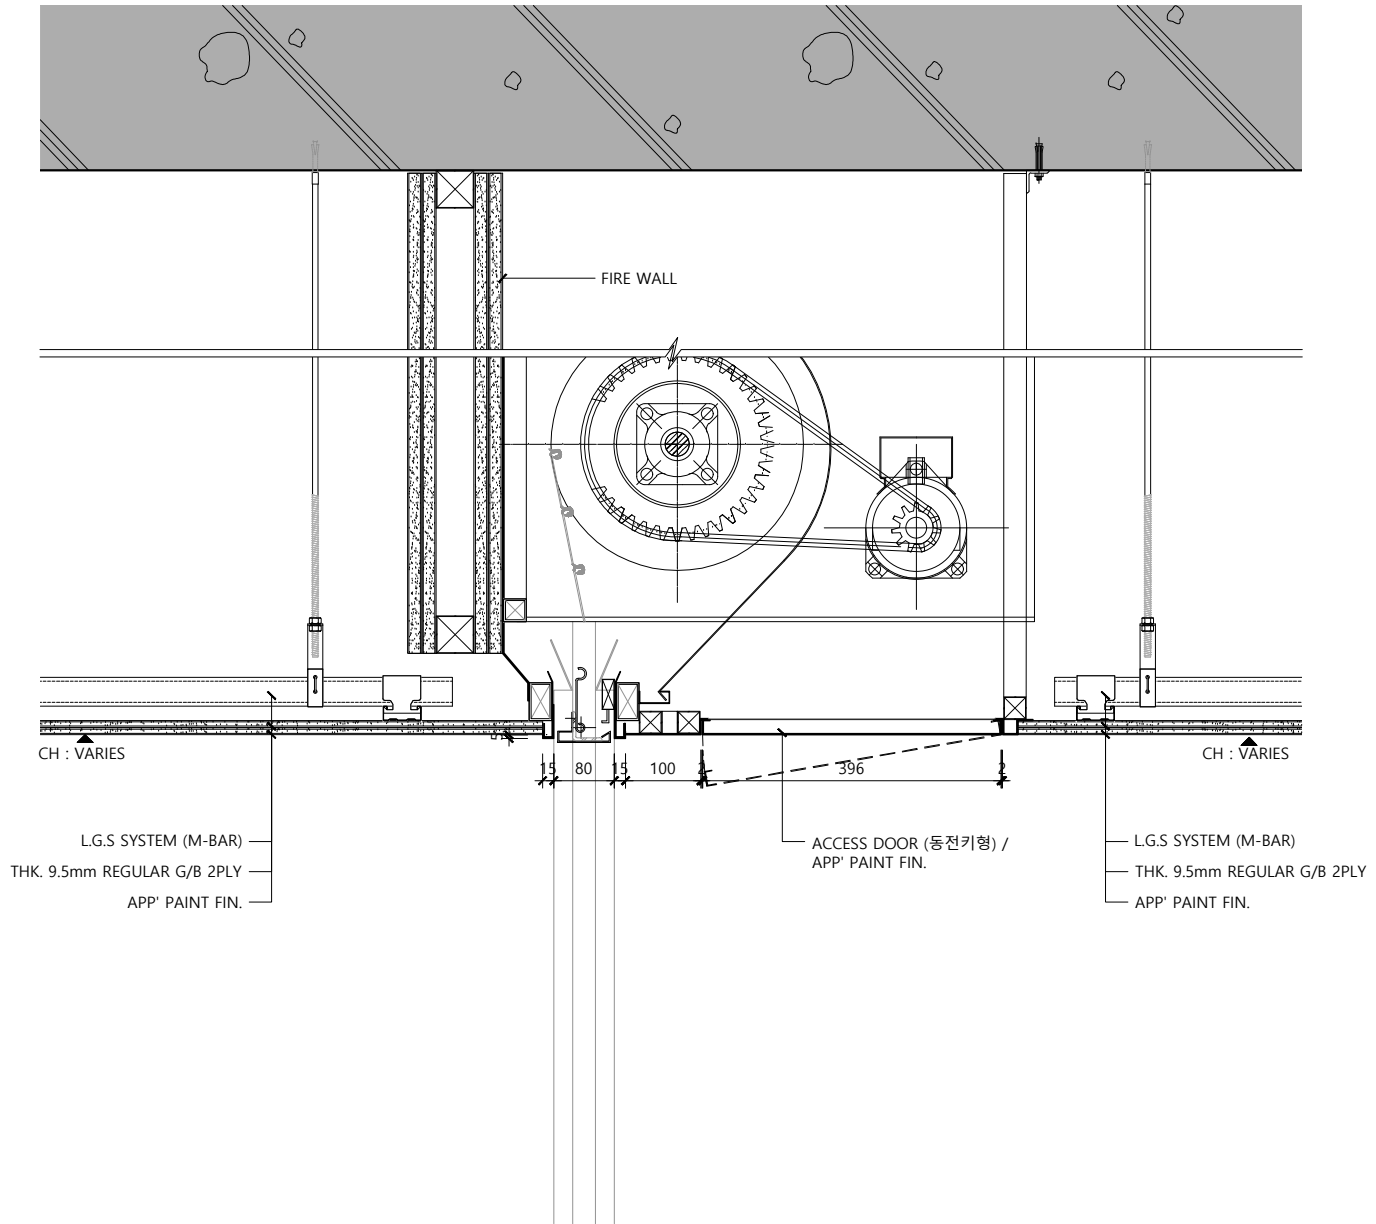
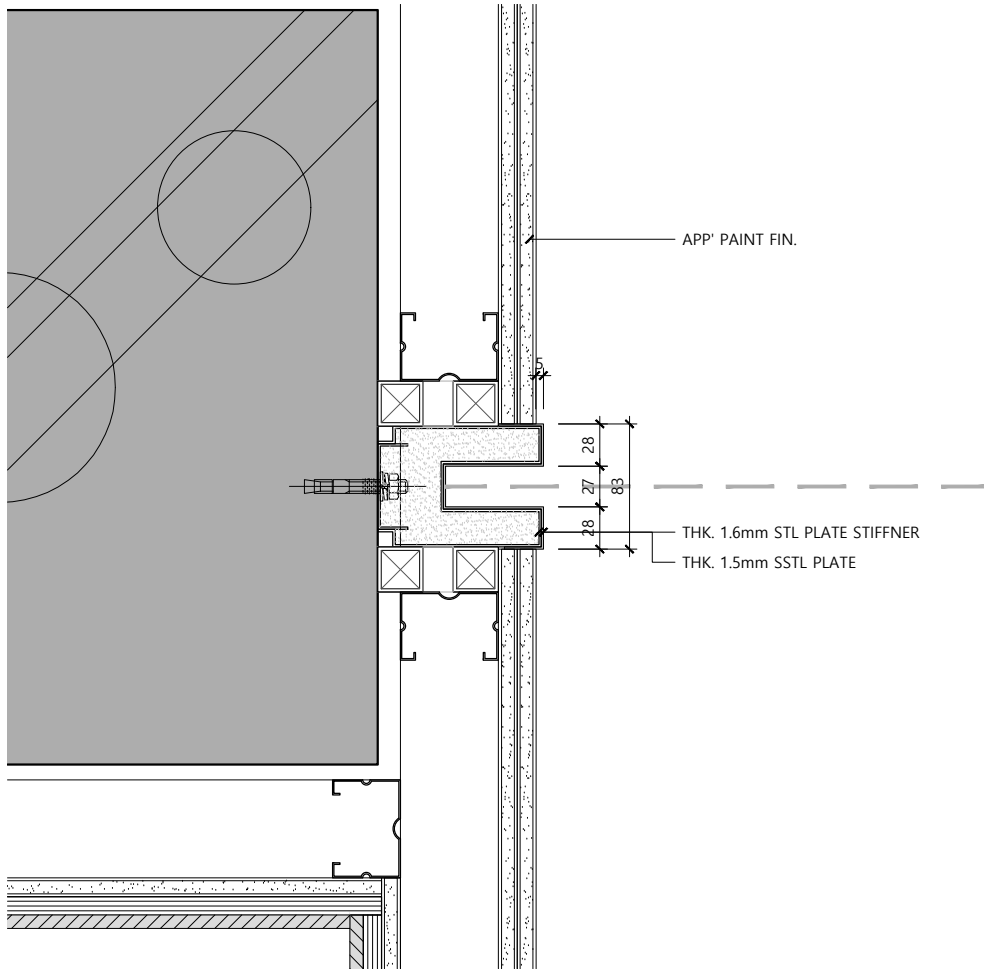
A3:1/10

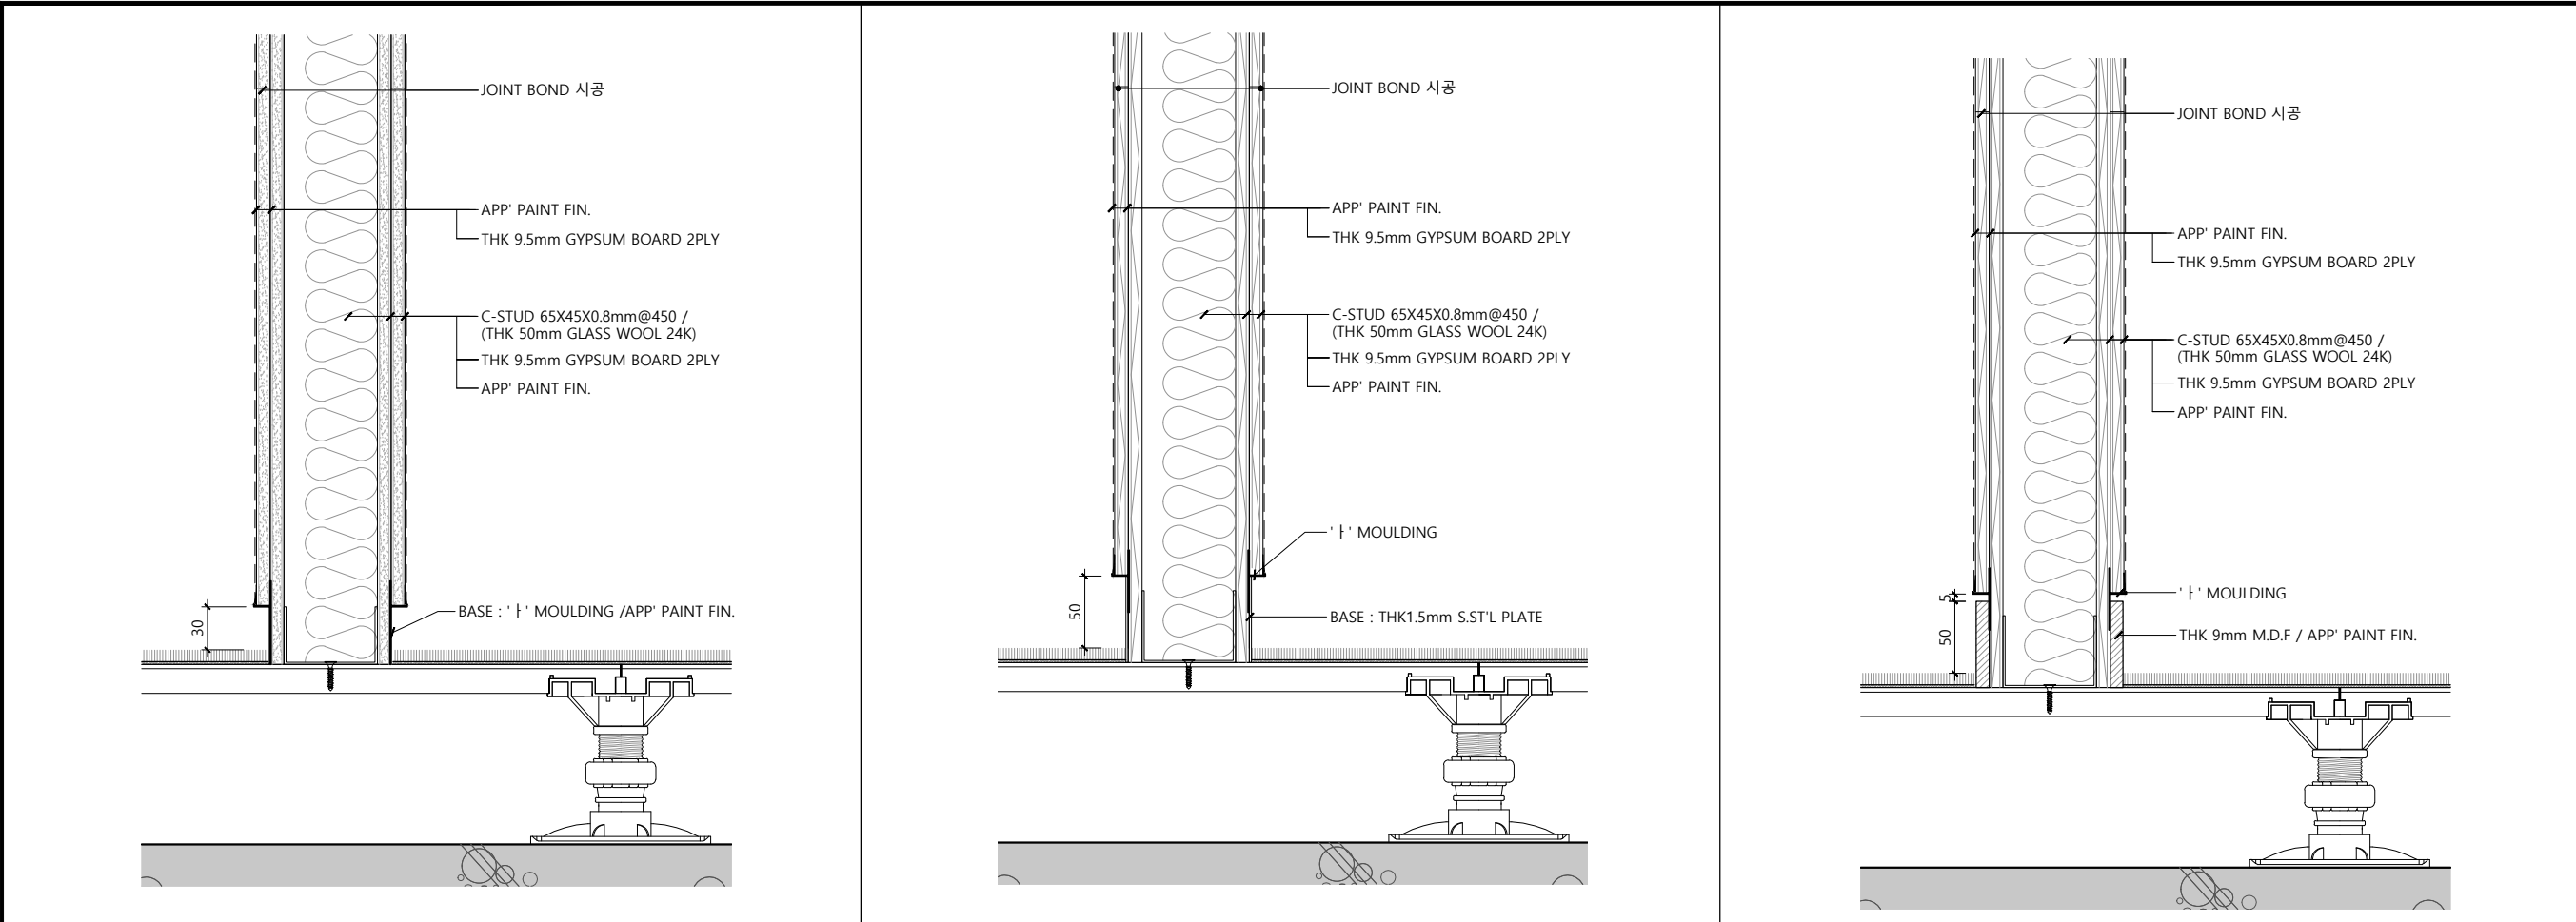
DRAWING NO.

CD-004


SHEET NO.

013





B(C)-001	FINISH	PAINT or INTERIOR FILM
	THK	-
B(C)-002	FINISH	METAL
	THK	-
B(C)-003	FINISH	(MDF) PAINT or INTERIOR FILM
	THK	-

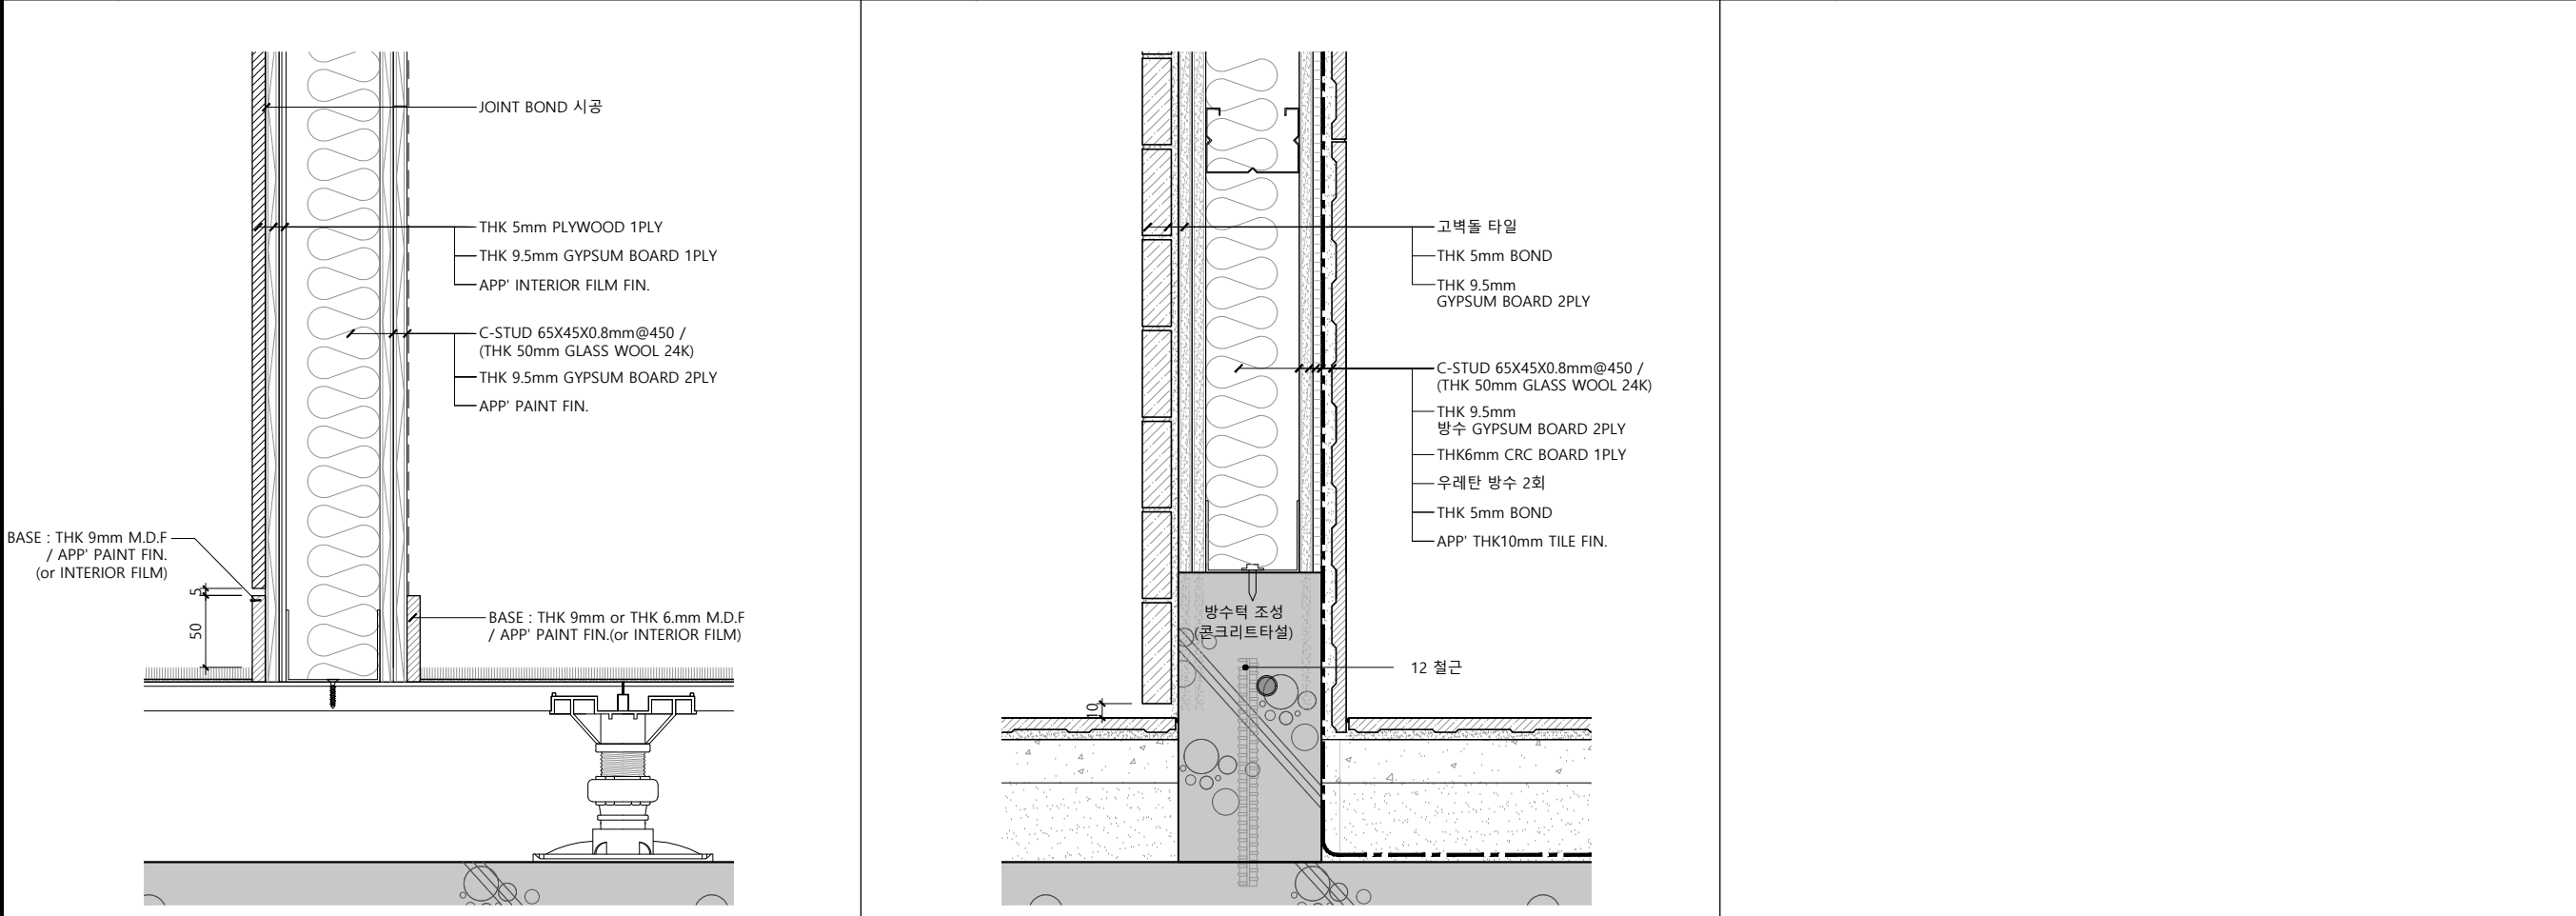

B(C)-004	FINISH	(MDF) PAINT or INTERIOR FILM
	THK	-
B-005	FINISH	TILE
	THK	-
-	FINISH	-
	THK	-

NAME OF CLIENT COMPANY

PROJECT TITLE

DETAIL
MANUAL

NOTE

매지몰딩 DJ-148 [인쇄]

대진알미늄 TEL : 02-2681-3100 , 2687-9100 , F
AX : 02-2682-6921

REV.	DATE	DESCRIPTION

NAME OF COMPANY

AJOUDESIGN GROUP

www.ajoudesign.co.kr

서울특별시 강동구 고덕비즈밸리로 6길10

10, Godeok Biz Valley-ro 6-gil, Gangdong-gu,

Seoul, Republic of Korea

DESIGN BY

-

DRAWING BY

-

CHECKED BY

-

DRAWING TITLE

걸레받이 상세도 -1

DATE

2025. 04.

SCALE

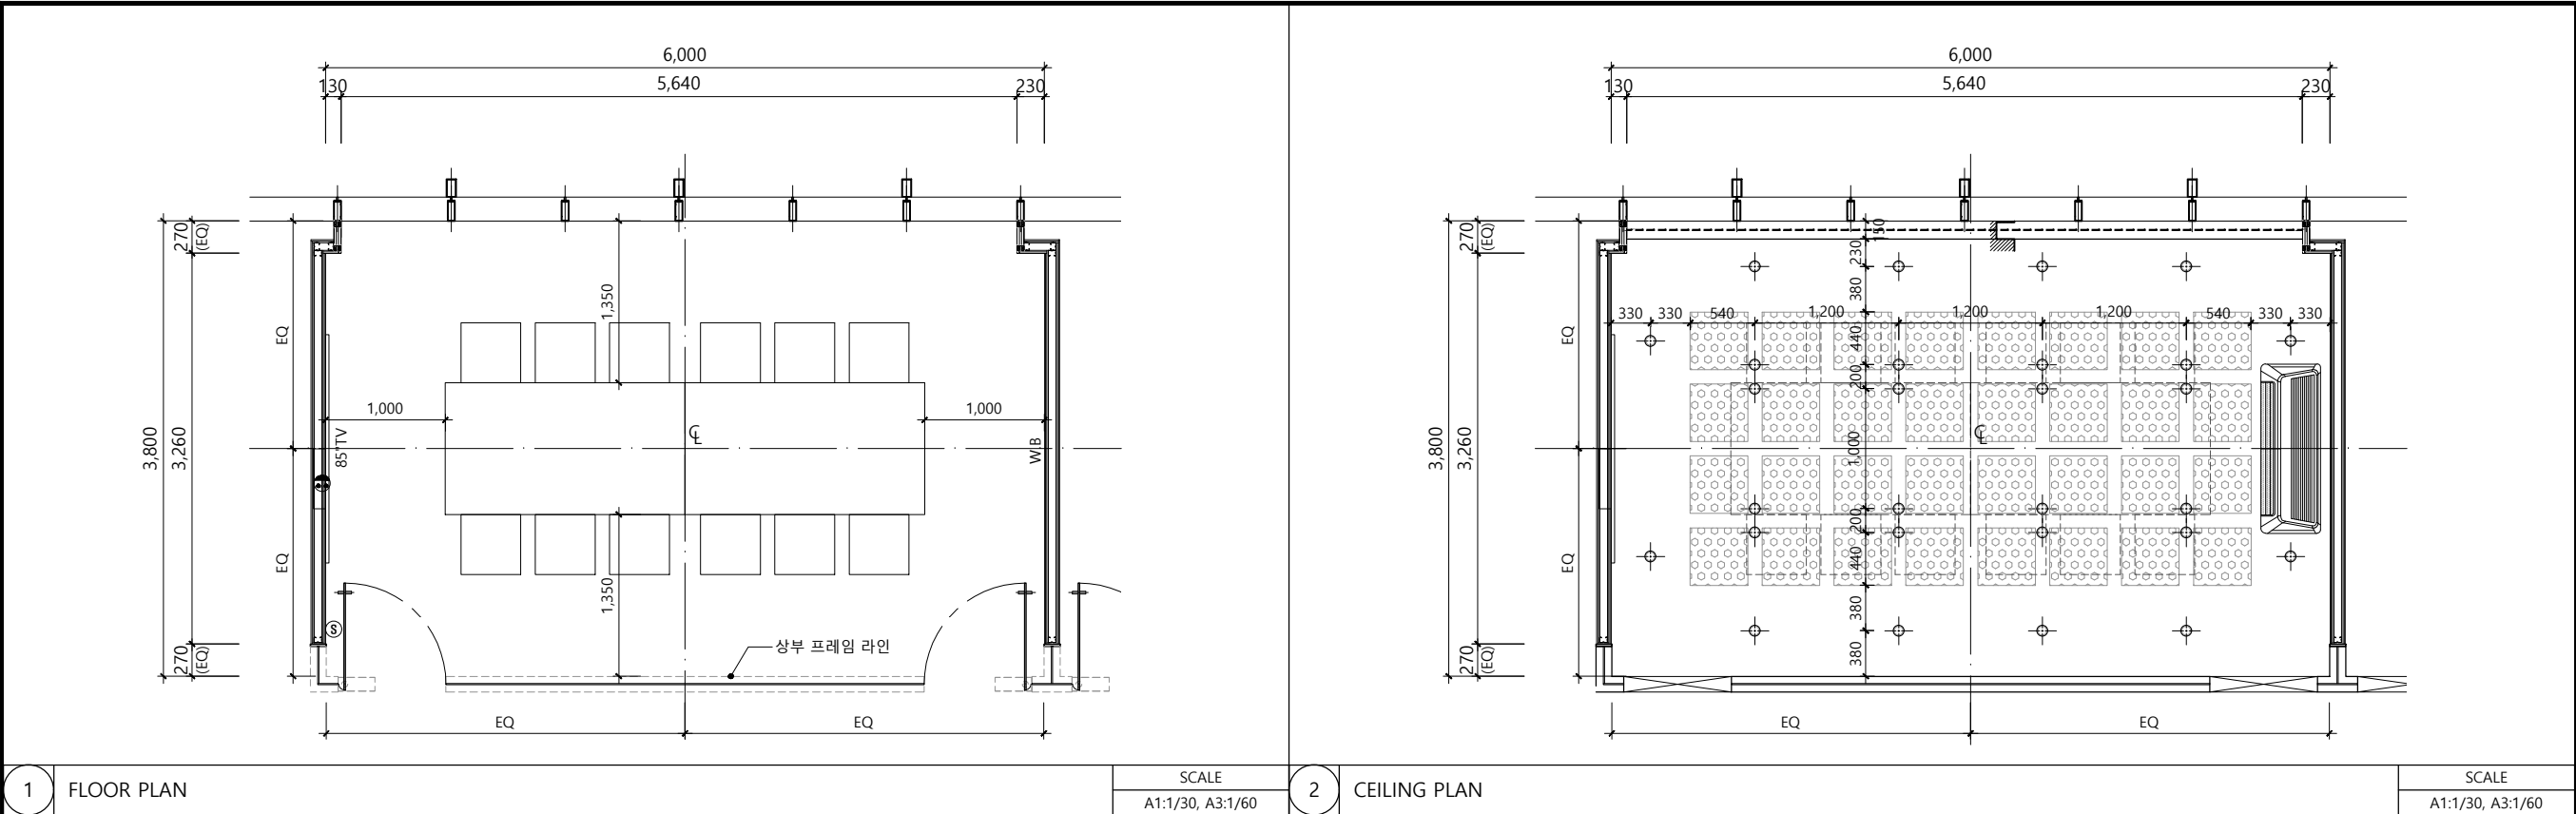
A3:1/ 5

DRAWING NO.

BD-001

SHEET NO.

017




1 FLOOR PLAN

SCALE
A1:1/30, A3:1/60

2 CEILING PLAN

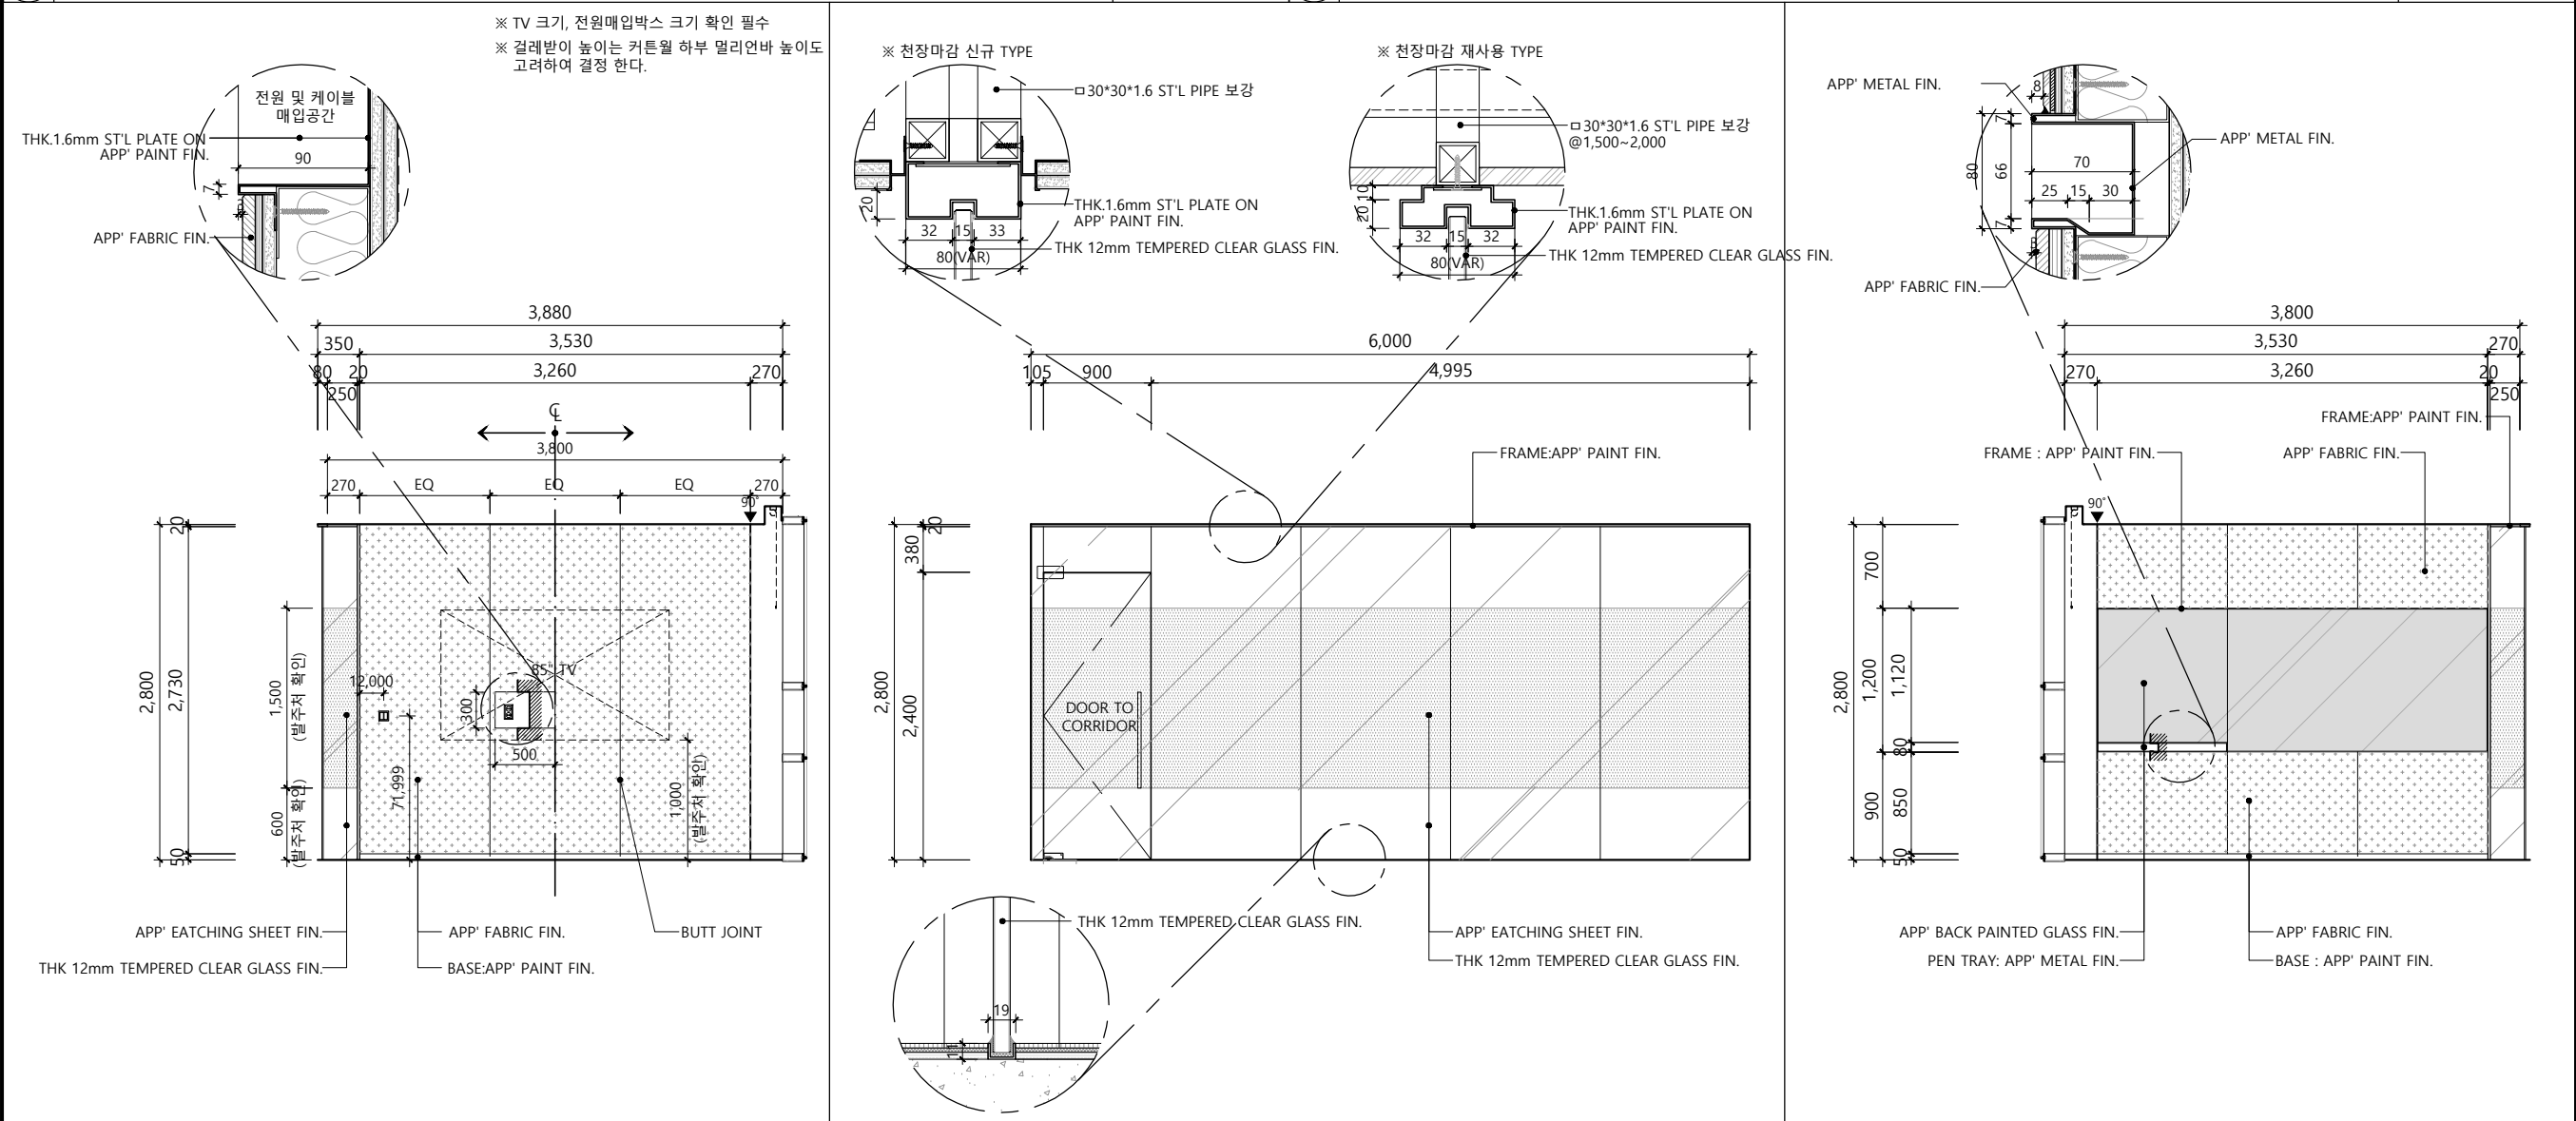SCALE
A1:1/30, A3:1/60



3 ELEVATION

SCALE
A1:1/30, A3:1/60

4 ELEVATION

SCALE
A1:1/30, A3:1/60

5 ELEVATION

SCALE
A1:1/30, A3:1/60

NAME OF CLIENT COMPANY

PROJECT TITLE

매뉴얼 설계

NOTE
이 도면은 설계 의도만을 나타내며 다른
컨설턴트의 도면과 비교 검토하여야 함.

1	-	-
REV.	DATE	DESCRIPTION

NAME OF COMPANY

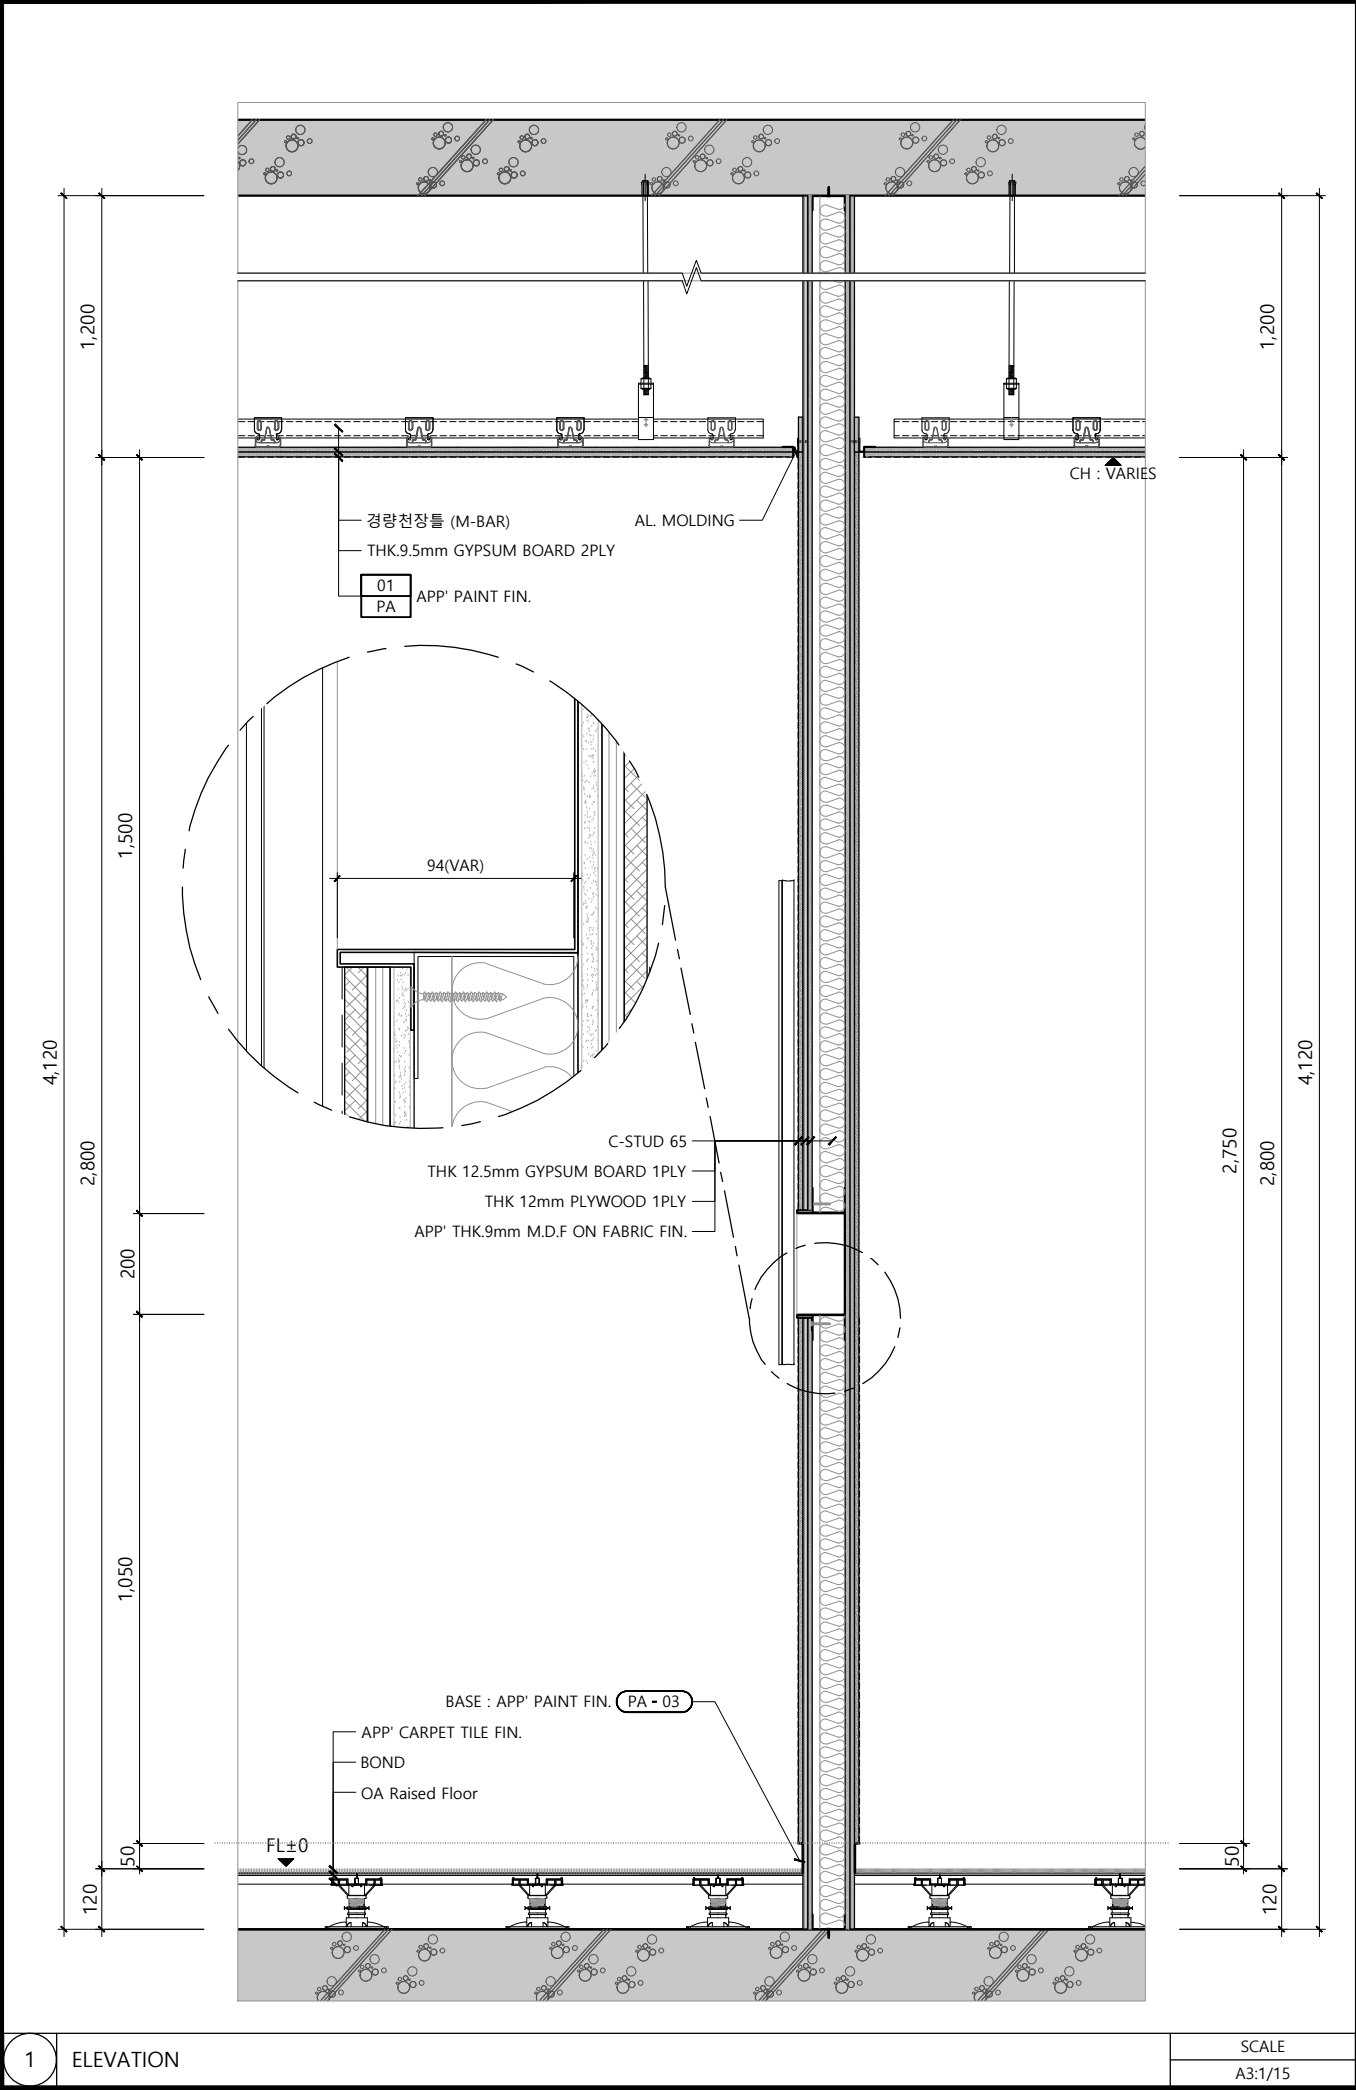


AJOUDESIGN GROUP
www.ajoudesign.co.kr
서울특별시 강동구 고덕비즈밸리로 6길10
10, Godeok Biz Valley-ro 6-gil, Gangdong-gu,
Seoul, Republic of Korea

DESIGN BY
DRAWING BY
CHECKED BY
DRAWING TITLE

회의실 예시

DATE
2025. 04.
SCALE
A1:1/30, A3:1/60
DRAWING NO.
EX-001
SHEET NO.
028



NAME OF CLIENT COMPANY

PROJECT TITLE

매뉴얼 설계

NOTE
이 도면은 설계 의도만을 나타내며 다른
컨설턴트의 도면과 비교 검토하여야 함.

REV.	DATE	DESCRIPTION
-	-	-
-	-	-
-	-	-
-	-	-

NAME OF COMPANY



AJOUDESIGN GROUP
www.ajoudesign.co.kr
서울특별시 강동구 고덕비즈밸리로 6길10
10, Godeok Biz Valley-ro 6-gil, Gangdong-gu,
Seoul, Republic of Korea

DESIGN BY

DRAWING BY

CHECKED BY

DRAWING TITLE

회의실 예시

DATE

2025. 04.

SCALE

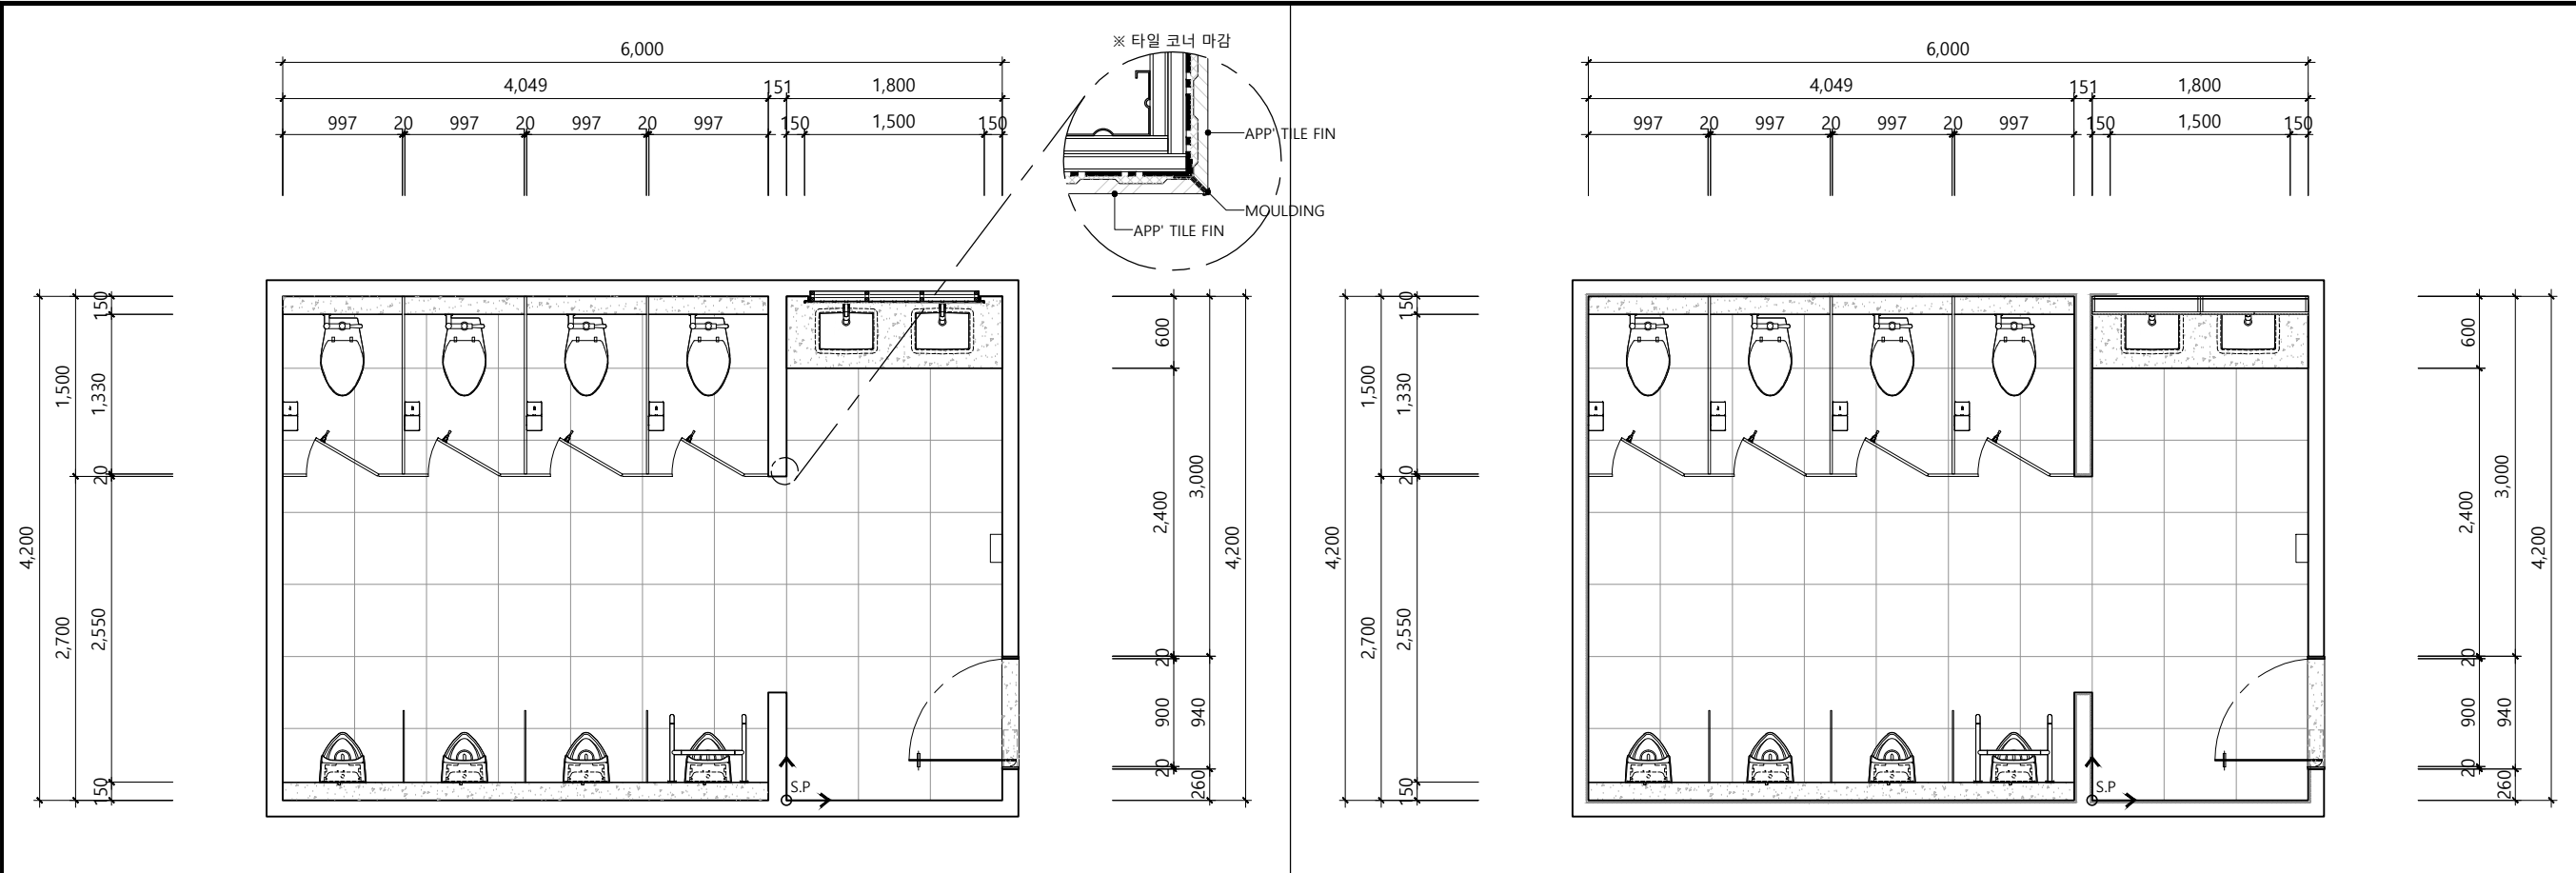
A3:1/15

DRAWING NO.

EX-002

SHEET NO.

029




1 FLOOR PLAN_ALT.1 [고정형 거울]

SCALE
A1:1/30, A3:1/60

2 FLOOR PLAN_ALT.2 [가구형 거울]

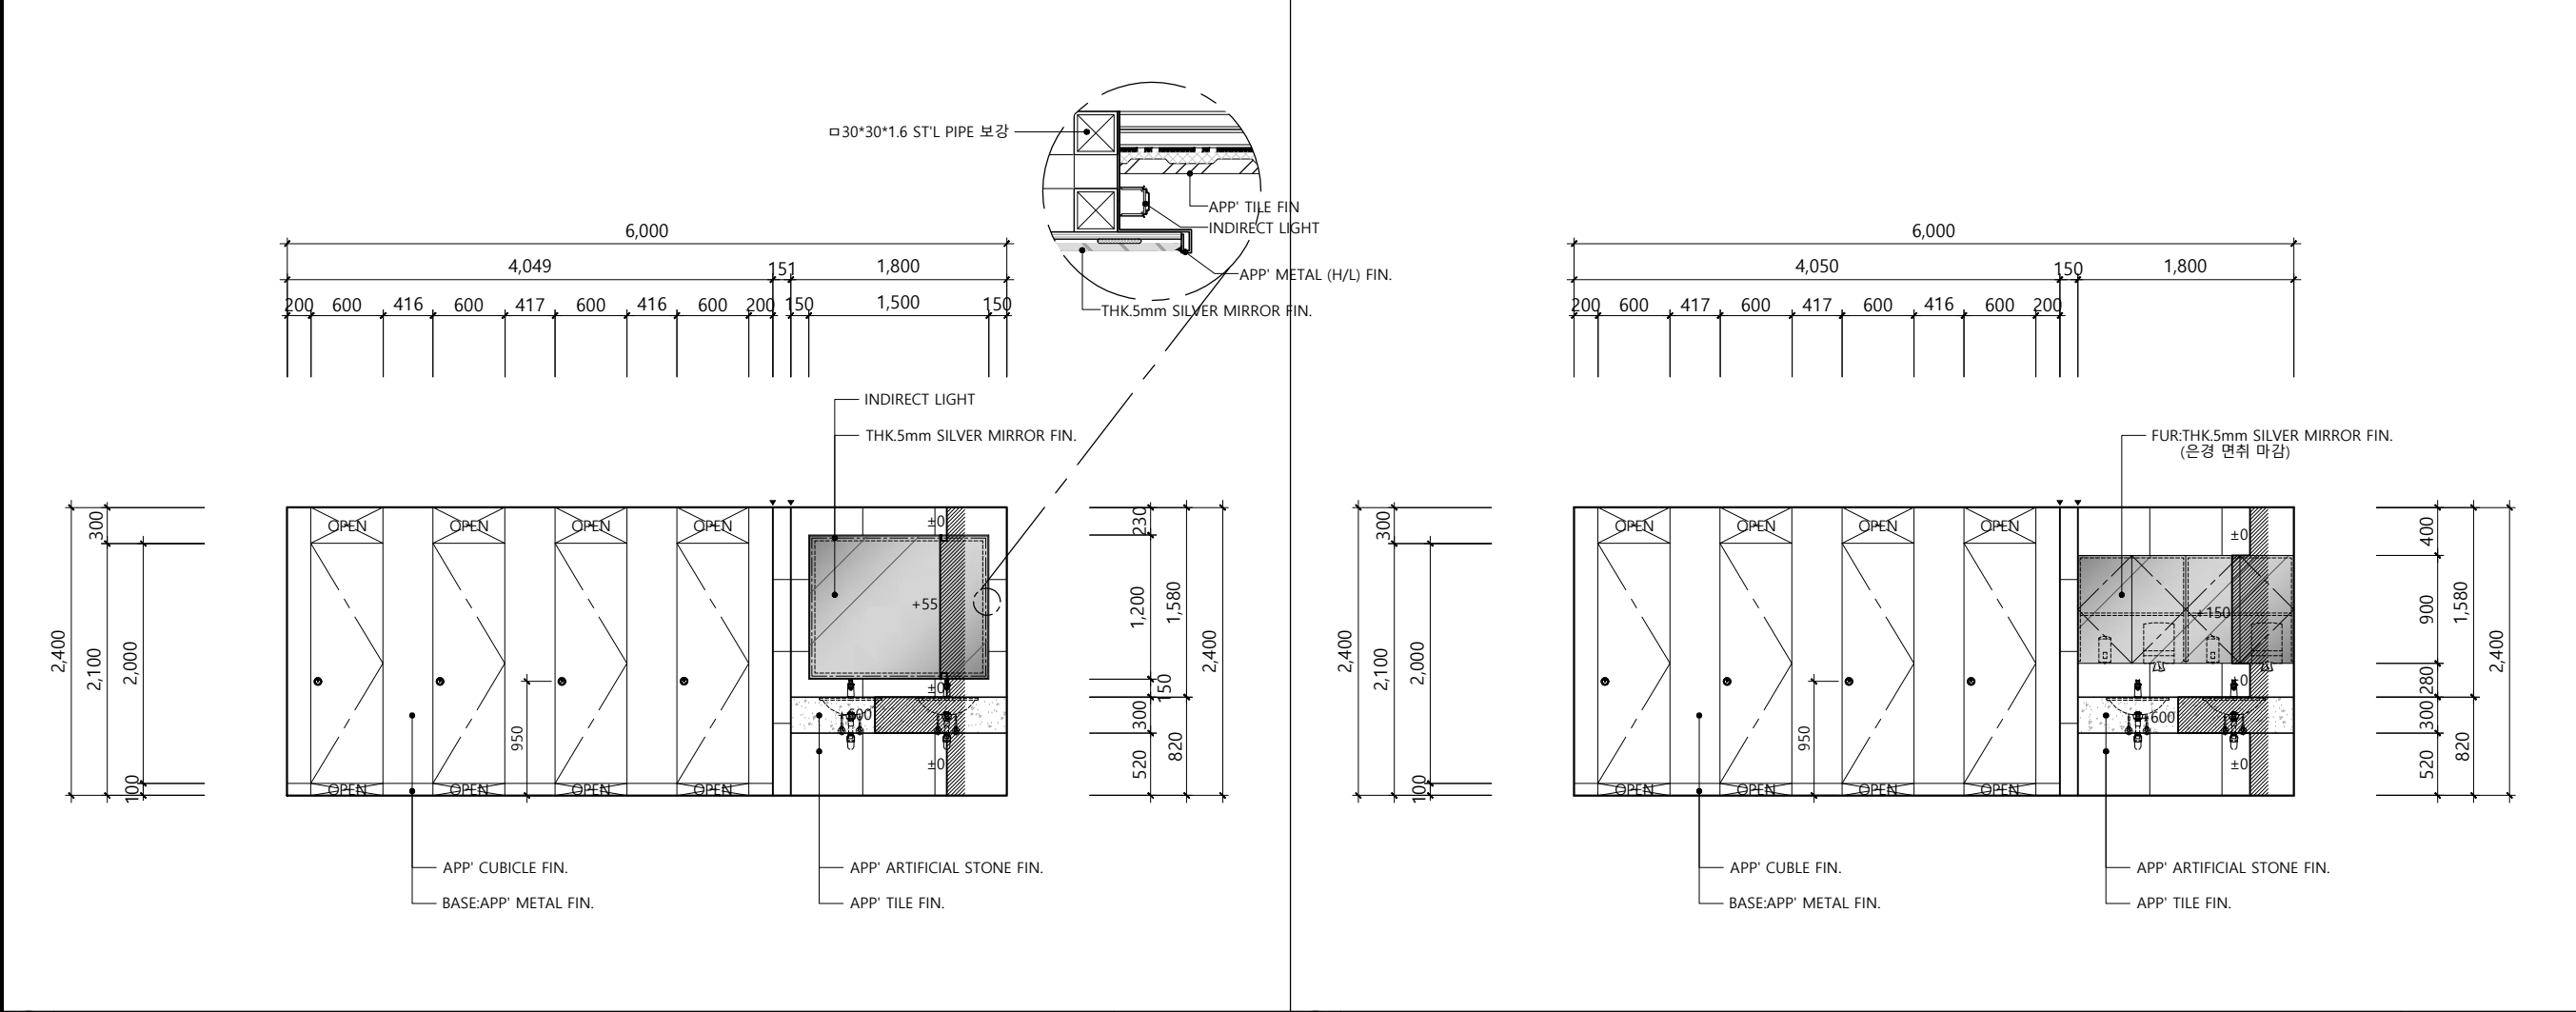SCALE
A1:1/30, A3:1/60



3 ELEVATION_ALT.1 [고정형 거울]

SCALE
A1:1/30, A3:1/60

4 ELEVATION_ALT.2 [가구형 거울]

SCALE
A1:1/30, A3:1/60

NAME OF CLIENT COMPANY

PROJECT TITLE

DETAIL
MANUAL

NOTE
이 도면은 설계 의도만을 나타내며 다른
컨설턴트의 도면과 비교 검토하여야 함.

-방수 높이(H): 1,500mm

REV.	DATE	DESCRIPTION
1	-	-

NAME OF COMPANY



AJOUDESIGN GROUP

www.ajoudesign.co.kr
서울특별시 강동구 고덕비즈밸리로 6길10
10, Godeok Biz Valley-ro 6-gil, Gangdong-gu,
Seoul, Republic of Korea

DESIGN BY

DRAWING BY

CHECKED BY

DRAWING TITLE

화장실 예시-1

DATE

2025. 04.

SCALE

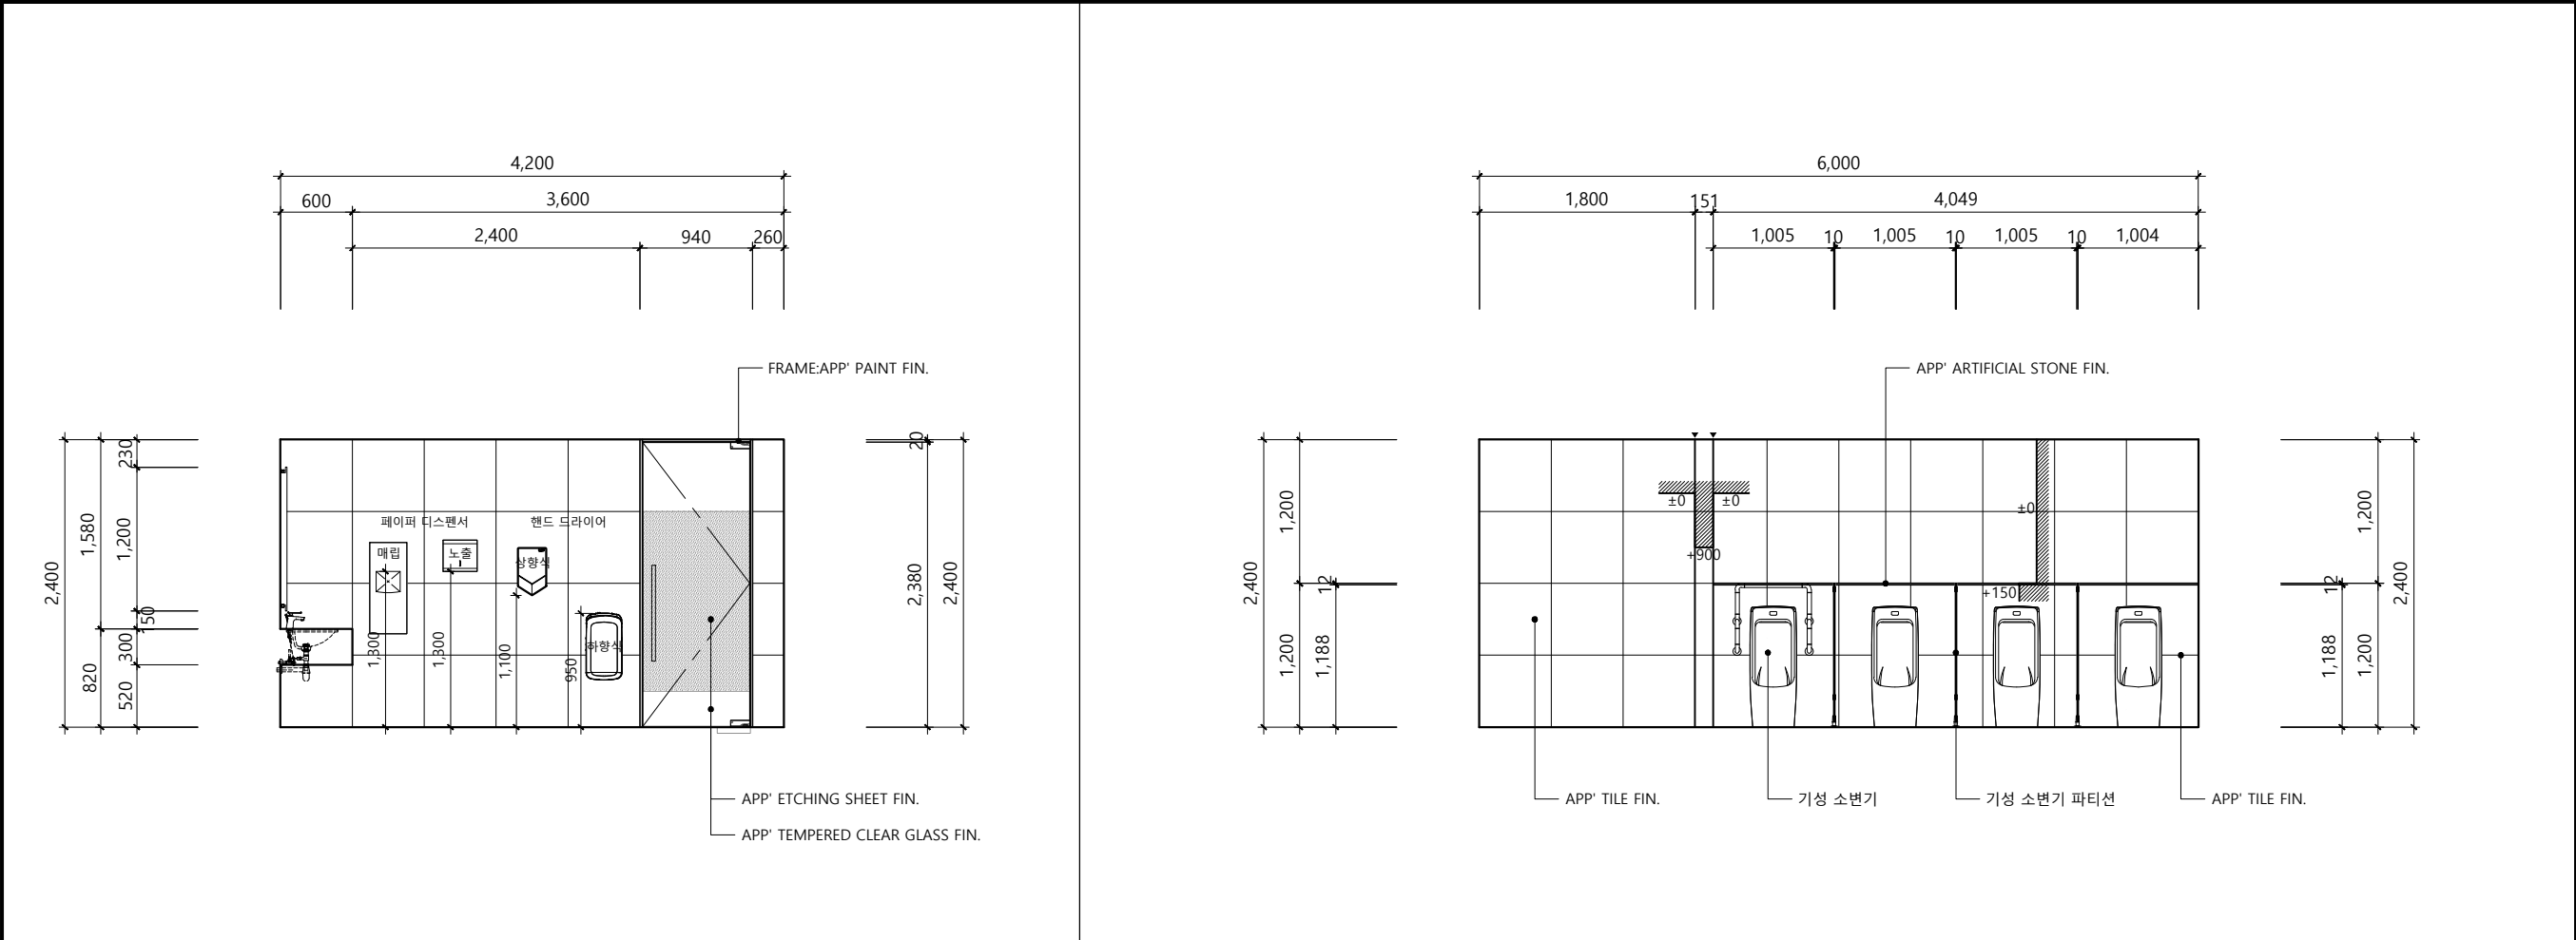
A1:1/30, A3:1/60

DRAWING NO.

EX-003

SHEET NO.

030




1 ELEVATION

SCALE
A1:1/30, A3:1/60

2 ELEVATION

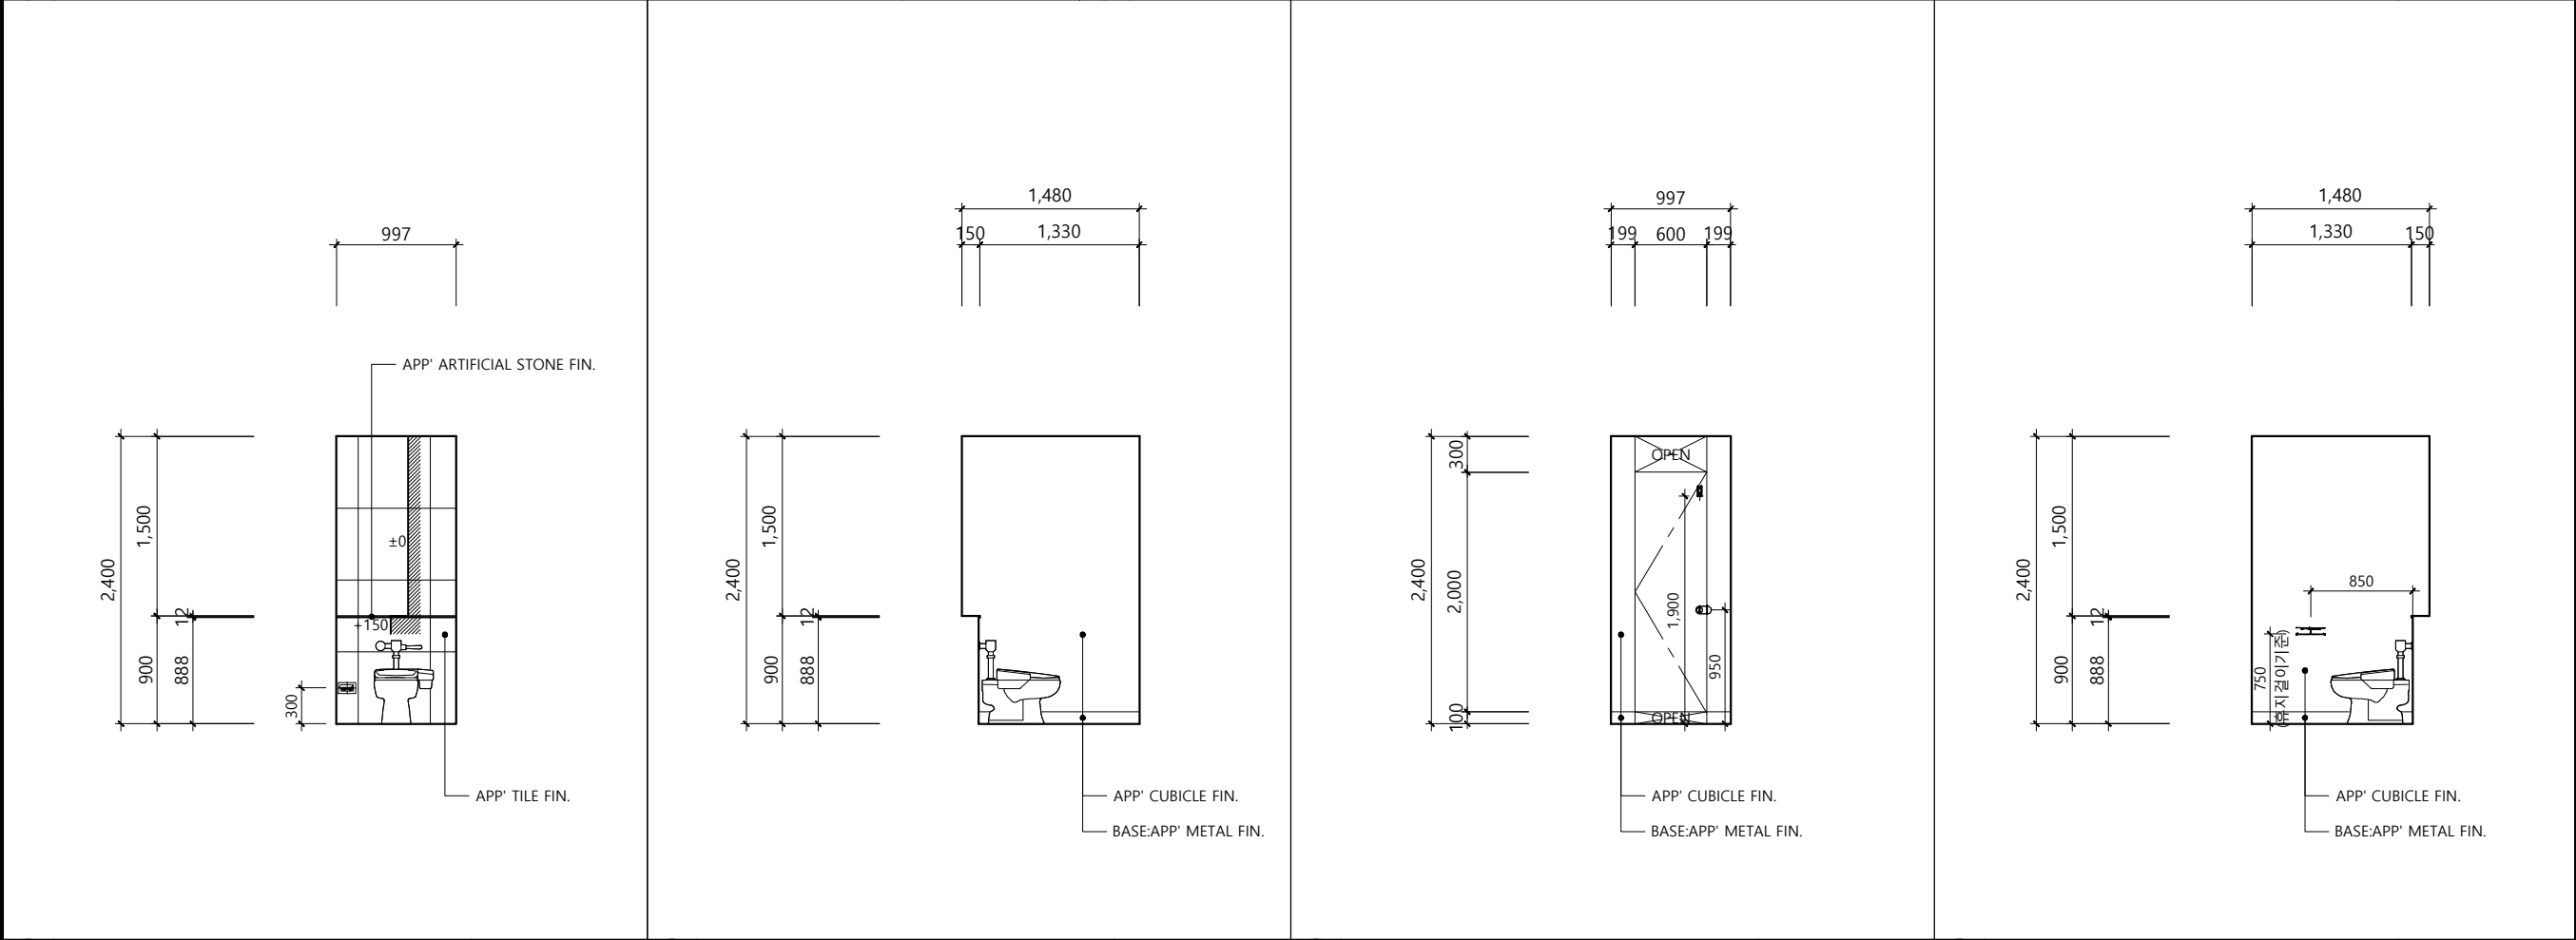SCALE
A1:1/30, A3:1/60



3 ELEVATION

SCALE
A1:1/30, A3:1/60

4 ELEVATION

SCALE
A1:1/30, A3:1/60

5 ELEVATION

SCALE
A1:1/30, A3:1/60

6 ELEVATION

SCALE
A1:1/30, A3:1/60

NAME OF CLIENT COMPANY

PROJECT TITLE

DETAIL
MANUAL

NOTE
이 도면은 설계 의도만을 나타내며 다른
컨설턴트의 도면과 비교 검토하여야 함.

1	-	-
REV.	DATE	DESCRIPTION

NAME OF COMPANY

AJOUDESIGN GROUP



www.ajoudesign.co.kr

서울특별시 강동구 고덕비즈밸리로 6길10
10, Godeok Biz Valley-ro 6-gil, Gangdong-gu,
Seoul, Republic of Korea

DESIGN BY	-
DRAWING BY	-
CHECKED BY	-
DRAWING TITLE	-

화장실 예시-1

DATE	2025. 04.
SCALE	A1:1/30, A3:1/60
DRAWING NO.	EX-004
SHEET NO.	031

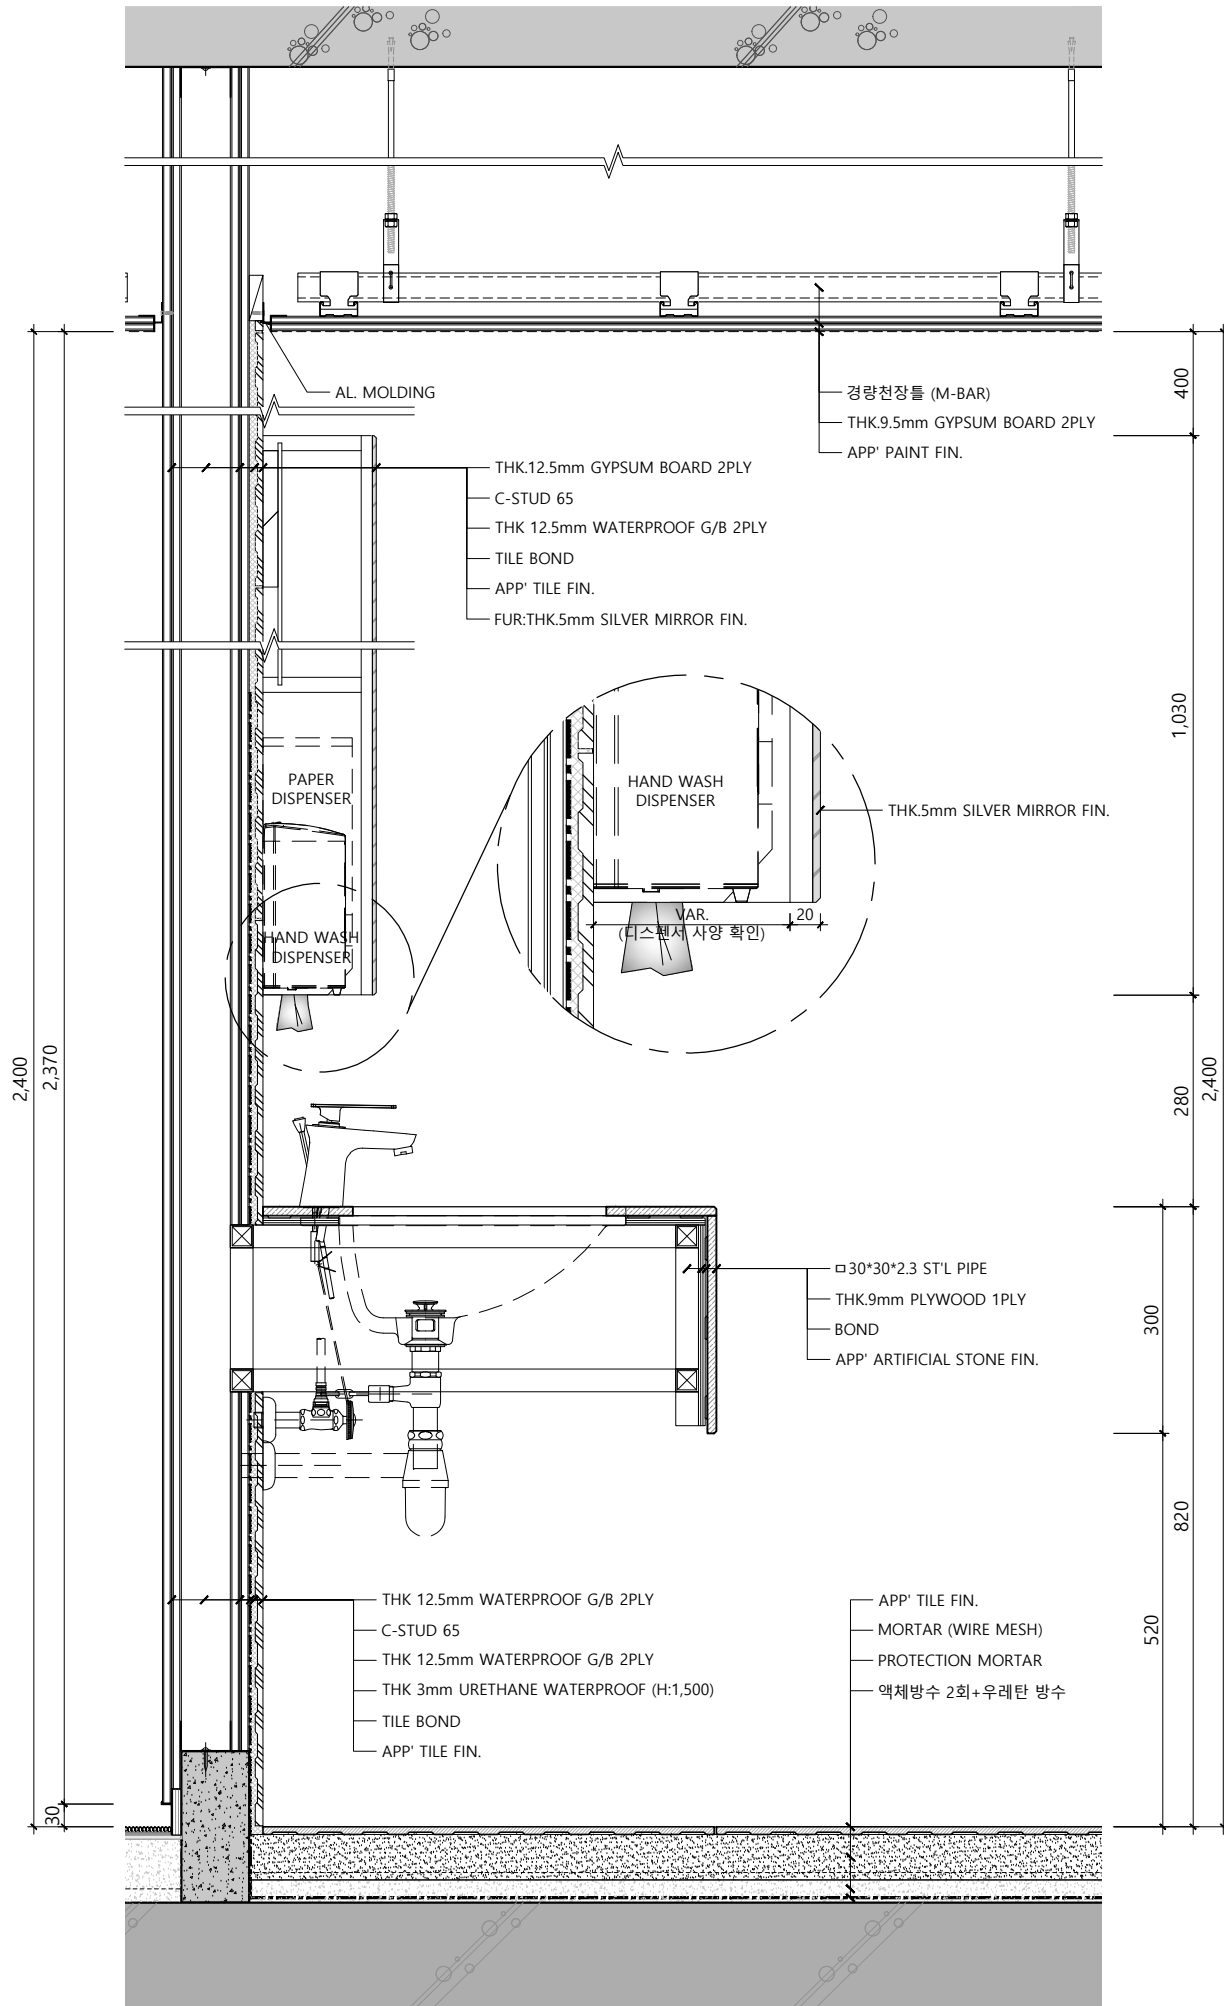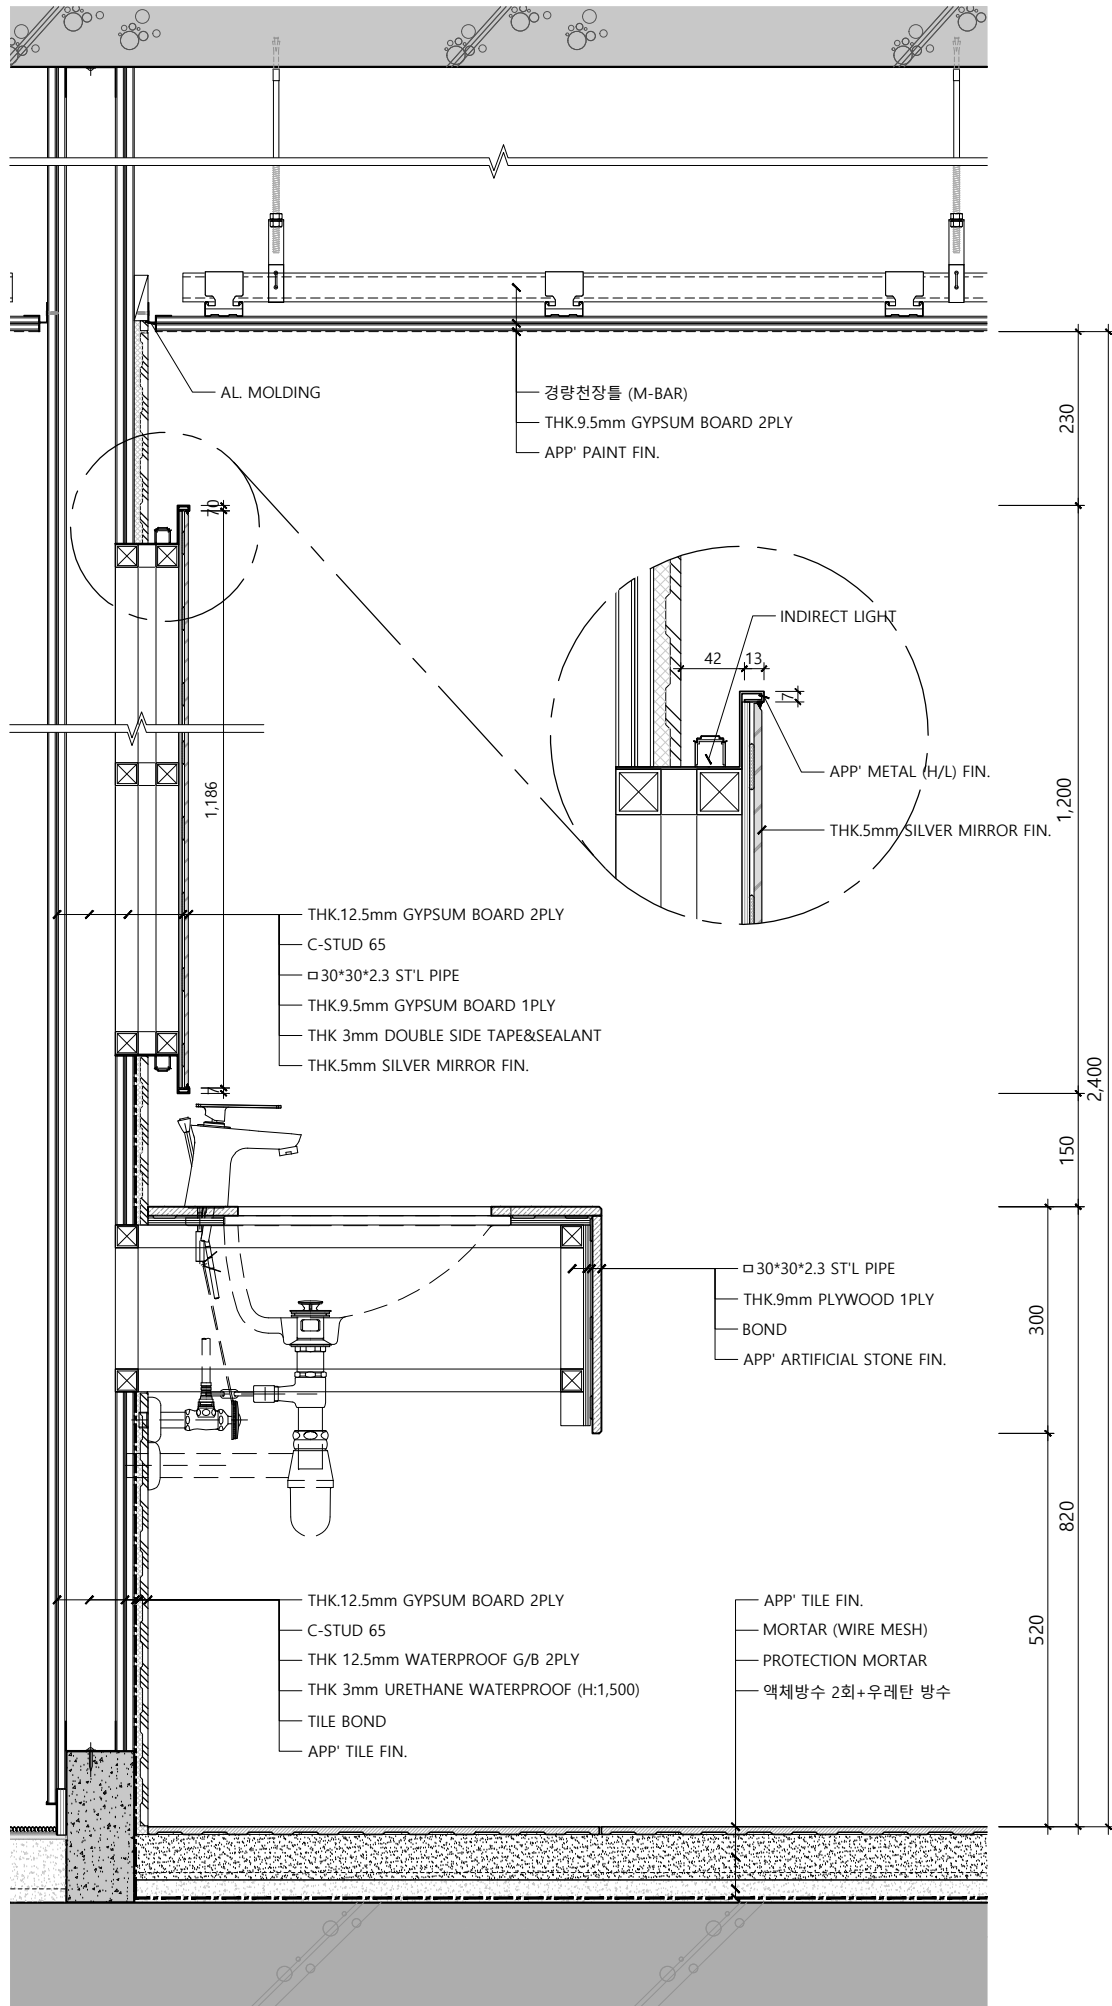

NAME OF CLIENT COMPANY

PROJECT TITLE

DETAIL MANUAL

NOTE
이 도면은 설계 의도만을 나타내며 다른
컨설턴트의 도면과 비교 검토하여야 함.

REV.	DATE	DESCRIPTION
1	-	-

NAME OF COMPANY



www.ajoudesign.co.kr
서울특별시 강동구 고덕비즈밸리로 6길10
10, Godeok Biz Valley-ro 6-gil, Gangdong-gu,
Seoul, Republic of Korea

DESIGN BY

DRAWING BY

CHECKED BY

DRAWING TITLE

화장실 예시-3

DATE

2025. 04.

SCALE

A1:1/5, A3:1/10

DRAWING NO.

EX-005

SHEET NO.

032